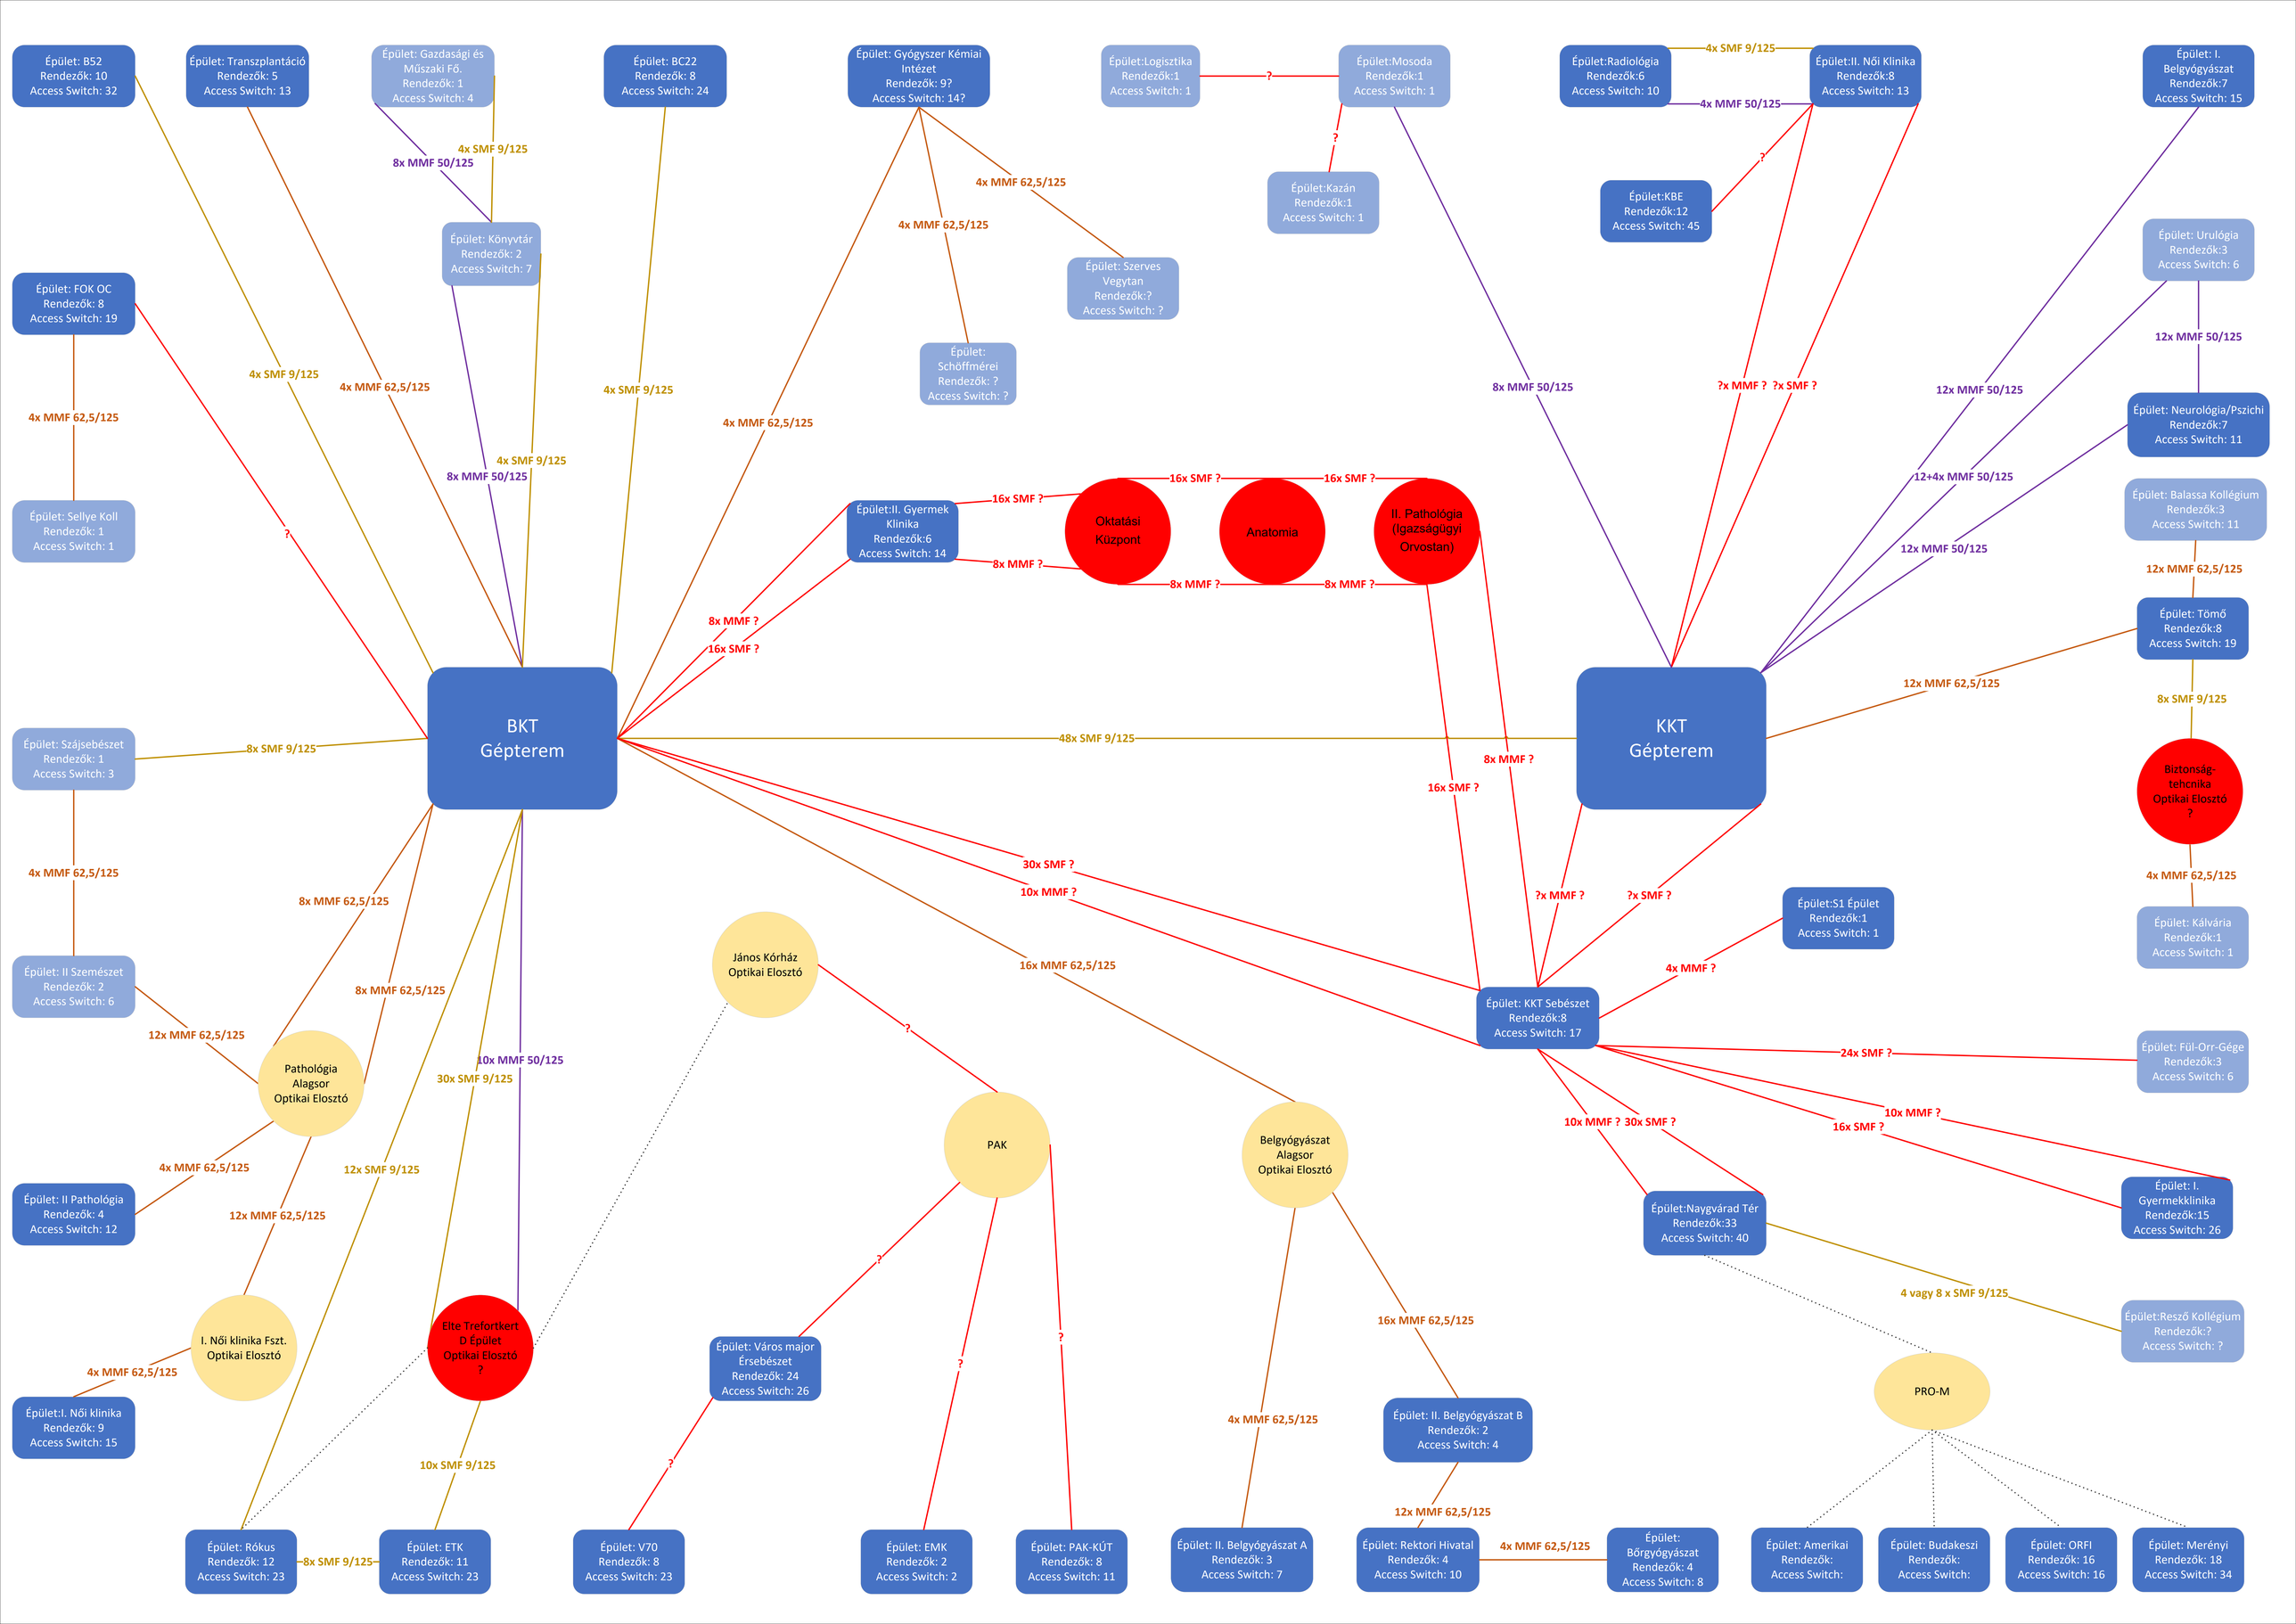
Épület: B52
Rendezők: 10
Access Switch: 32
Épület: Transzplantáció
Rendezők: 5
Access Switch: 13
Épület: Gazdasági és Műszaki Fő.
Rendezők: 1
Access Switch: 4
Épület: BC22
Rendezők: 8
Access Switch: 24
Épület: Gyógyszer Kémiai Intézet
Rendezők: 9?
Access Switch: 14?
Épület:Logisztika
Rendezők:1
Access Switch: 1
Épület:Mosoda
Rendezők:1
Access Switch: 1
Épület:Radiológia
Rendezők:6
Access Switch: 10
Épület:II. Női Klinika
Rendezők:8
Access Switch: 13
Épület: I. Belgyógyászat
Rendezők:7
Access Switch: 15
4x SMF 9/125
4x MMF 50/125
8x MMF 50/125
4x SMF 9/125
Épület: Könyvtár
Rendezők: 2
Access Switch: 7
4x MMF 62,5/125
4x MMF 62,5/125
Épület: Szerves Vegytan
Rendezők:?
Access Switch: ?
Épület:Kazán
Rendezők:1
Access Switch: 1
Épület:KBE
Rendezők:12
Access Switch: 45
Épület: Urológia
Rendezők:3
Access Switch: 6
Épület: FOK OC
Rendezők: 8
Access Switch: 19
4x SMF 9/125
4x MMF 62,5/125
4x SMF 9/125
Épület: Schöffmérei
Rendezők: ?
Access Switch: ?
8x MMF 50/125
?x MMF ? ?x SMF ?
12x MMF 50/125
12x MMF 50/125
4x MMF 62,5/125
4x SMF 9/125
8x MMF 50/125
Épület: Neurológia/Pszichi
Rendezők:7
Access Switch: 11
Épület: Sellye Koll
Rendezők: 1
Access Switch: 1
Épület:II. Gyermek Klinika
Rendezők:6
Access Switch: 14
16x SMF ?
8x MMF ?
Oktatási Küzpont
16x SMF ?
Anatomia
16x SMF ?
II. Pathológia (Igazságügyi Orvostan)
8x MMF ?
8x MMF ?
12+4x MMF 50/125
Épület: Balassa Kollégium
Rendezők:3
Access Switch: 11
12x MMF 50/125
12x MMF 62,5/125
Épület: Tömő
Rendezők:8
Access Switch: 19
8x MMF ?
16x SMF ?
BKT Gépterem
48x SMF 9/125
KKT Gépterem
12x MMF 62,5/125
8x SMF 9/125
Épület: Szájsebészet
Rendezők: 1
Access Switch: 3
8x SMF 9/125
8x MMF ?
16x SMF ?
Biztonság-tehcnika Optikai Elosztó ?
30x SMF ?
10x MMF ?
4x MMF 62,5/125
4x MMF 62,5/125
8x MMF 62,5/125
?x MMF ?
?x SMF ?
Épület:S1 Épület
Rendezők:1
Access Switch: 1
Épület: Kálvária
Rendezők:1
Access Switch: 1
János Kórház Optikai Elosztó
16x MMF 62,5/125
4x MMF ?
Épület: II Szemészet
Rendezők: 2
Access Switch: 6
8x MMF 62,5/125
8x MMF 62,5/125
Épület: KKT Sebészet
Rendezők:8
Access Switch: 17
12x MMF 62,5/125
Pathológia Alagsor Optikai Elosztó
10x MMF 50/125
30x SMF 9/125
24x SMF ?
Épület: Fül-Orr-Gége
Rendezők:3
Access Switch: 6
PAK
Belgyógyászat Alagsor Optikai Elosztó
10x MMF ? 30x SMF ?
10x MMF ?
16x SMF ?
4x MMF 62,5/125
12x SMF 9/125
Épület: II Pathológia
Rendezők: 4
Access Switch: 12
12x MMF 62,5/125
Épület:Naygvárad Tér
Rendezők:33
Access Switch: 40
Épület: I. Gyermekklinika
Rendezők:15
Access Switch: 26
4 vagy 8 x SMF 9/125
Épület:Resző Kollégium
Rendezők:?
Access Switch: ?
I. Női klinika Fszt. Optikai Elosztó
Elte Trefortkert D Épület Optikai Elosztó ?
Épület: Város major Érsebészet
Rendezők: 24
Access Switch: 26
16x MMF 62,5/125
4x MMF 62,5/125
PRO-M
4x MMF 62,5/125
Épület:I. Női klinika
Rendezők: 9
Access Switch: 15
Épület: II. Belgyógyászat B
Rendezők: 2
Access Switch: 4
10x SMF 9/125
12x MMF 62,5/125
Épület: Rókus
Rendezők: 12
Access Switch: 23
8x SMF 9/125
Épület: ETK
Rendezők: 11
Access Switch: 23
Épület: V70
Rendezők: 8
Access Switch: 23
Épület: EMK
Rendezők: 2
Access Switch: 2
Épület: PAK-KÚT
Rendezők: 8
Access Switch: 11
Épület: II. Belgyógyászat A
Rendezők: 3
Access Switch: 7
Épület: Rektori Hivatal
Rendezők: 4
Access Switch: 10
4x MMF 62,5/125
Épület: Bőrgyógyászat
Rendezők: 4
Access Switch: 8
Épület: Amerikai
Rendezők:
Access Switch:
Épület: Budakeszi
Rendezők:
Access Switch:
Épület: ORFI
Rendezők: 16
Access Switch: 16
Épület: Merényi
Rendezők: 18
Access Switch: 34

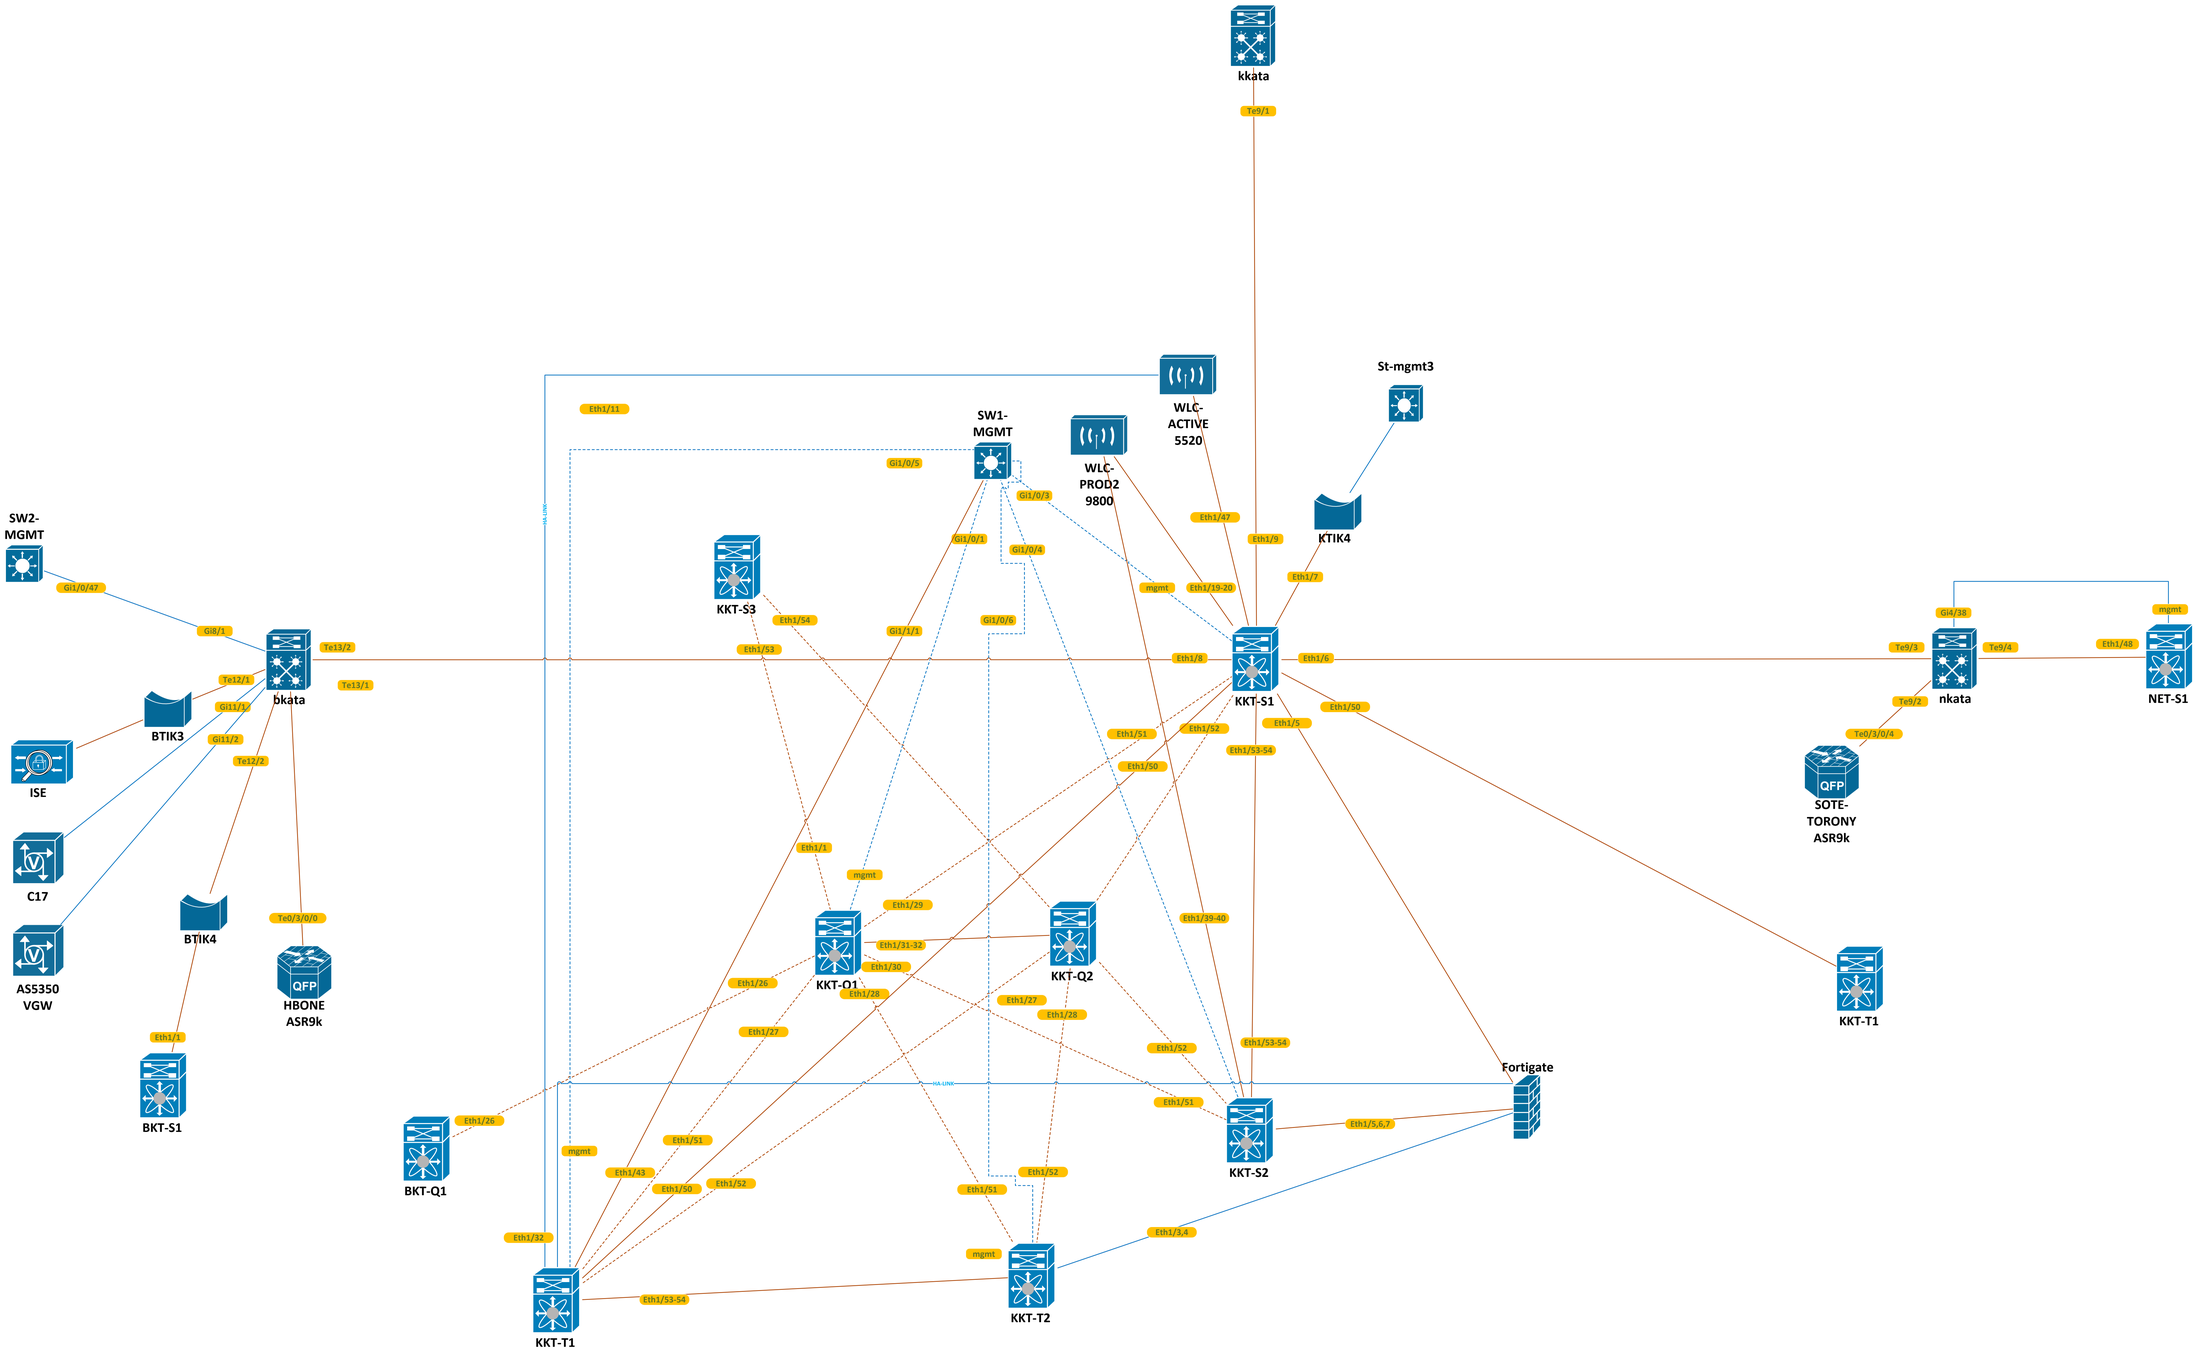
kkata
Te9/1
WLC-ACTIVE 5520
St-mgmt3
KTIK4
Eth1/11
SW1-MGMT
Gi1/0/5
WLC-PROD2 9800
Gi1/0/3
Eth1/47
Eth1/9
Gi1/0/1
Gi1/0/4
Eth1/7
mgmt
Eth1/19-20
SW2-MGMT
Gi1/0/47
KKT-S3
Eth1/54
Gi1/1/1
Gi1/0/6
Eth1/53
Eth1/8
Eth1/6
Gi8/1
Te13/2
Te13/1
Te12/1
Gi11/1
bkata
BTIK3
Gi11/2
Te12/2
ISE
C17
AS5350 VGW
BTIK4
Te0/3/0/0
HBONE ASR9k
Eth1/1
BKT-S1
KKT-S1
Eth1/50
Eth1/51
Eth1/52
Eth1/5
Eth1/53-54
Eth1/50
Gi4/38
mgmt
Te9/3
Te9/4
Eth1/48
nkata
NET-S1
Te9/2
Te0/3/0/4
SOTE-TORONY ASR9k
Eth1/1
mgmt
Eth1/29
Eth1/31-32
Eth1/30
Eth1/28
KKT-O1
KKT-Q2
Eth1/39-40
Eth1/26
Eth1/27
Eth1/28
Eth1/27
Eth1/52
Eth1/53-54
KKT-T1
HA LINK
Fortigate
Eth1/51
Eth1/5,6,7
KKT-S2
Eth1/26
BKT-Q1
mgmt
Eth1/51
Eth1/43
Eth1/50
Eth1/52
Eth1/51
Eth1/52
Eth1/32
Eth1/3,4
mgmt
Eth1/53-54
KKT-T1
KKT-T2

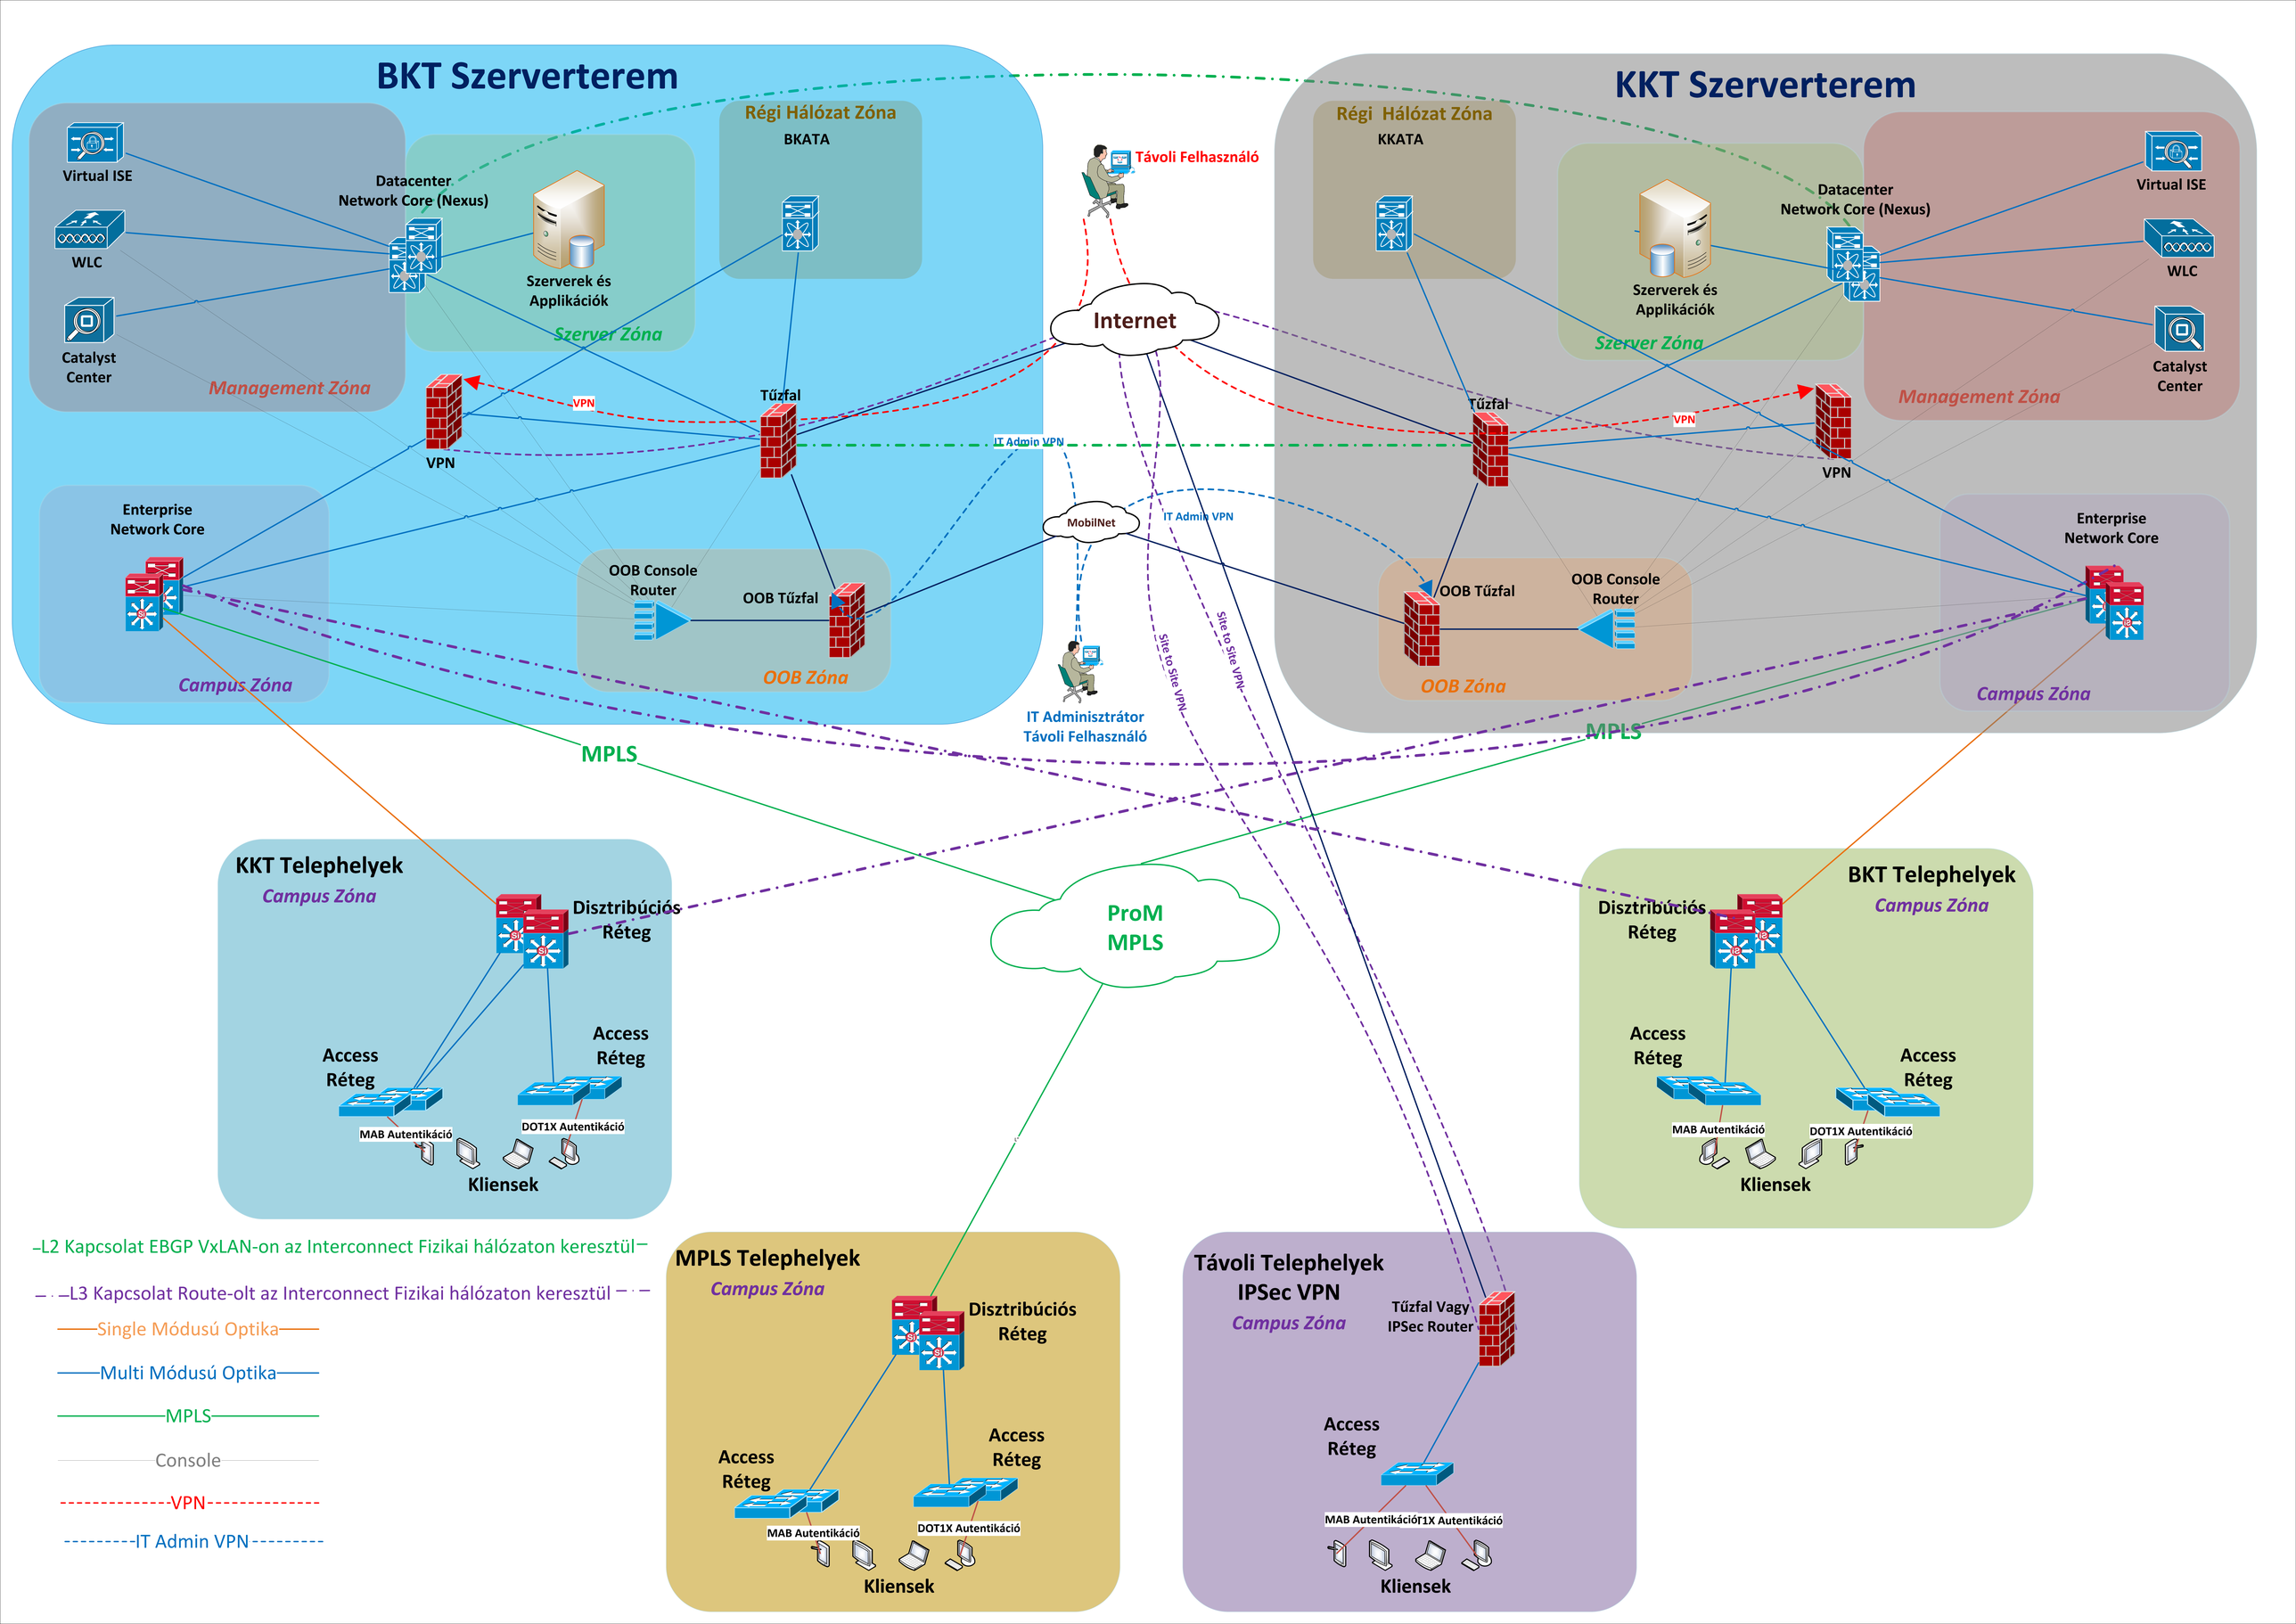
BKT Szerverterem
Régi Hálózat Zóna
BKATA
Virtual ISE
WLC
Catalyst Center
Datacenter Network Core (Nexus)
Szerverek és Applikációk
Szerver Zóna
Management Zóna
VPN
Tűzfal
Enterprise Network Core
OOB Console Router
OOB Tűzfal
OOB Zóna
Campus Zóna
Távoli Felhasználó
Internet
IT Admin VPN
MobilNet
IT Adminisztrátor Távoli Felhasználó
Site to Site VPN
KKT Szerverterem
Régi Hálózat Zóna
KKATA
Szerverek és Applikációk
Szerver Zóna
Datacenter Network Core (Nexus)
Virtual ISE
WLC
Catalyst Center
Management Zóna
Tűzfal
VPN
OOB Tűzfal
OOB Console Router
OOB Zóna
Enterprise Network Core
Campus Zóna
MPLS
KKT Telephelyek
Campus Zóna
Disztribúciós Réteg
Access Réteg
MAB Autentikáció
DOT1X Autentikáció
Kliensek
ProM MPLS
BKT Telephelyek
Campus Zóna
Disztribúciós Réteg
Access Réteg
MAB Autentikáció
DOT1X Autentikáció
Kliensek
MPLS Telephelyek
Campus Zóna
Disztribúciós Réteg
Access Réteg
MAB Autentikáció
DOT1X Autentikáció
Kliensek
Távoli Telephelyek IPSec VPN
Campus Zóna
Tűzfal Vagy IPSec Router
Access Réteg
MAB Autentikáció
DOT1X Autentikáció
Kliensek
L2 Kapcsolat EBGP VxLAN-on az Interconnect Fizikai hálózaton keresztül
L3 Kapcsolat Route-olt az Interconnect Fizikai hálózaton keresztül
Single Módusú Optika
Multi Módusú Optika
MPLS
Console
VPN
IT Admin VPN

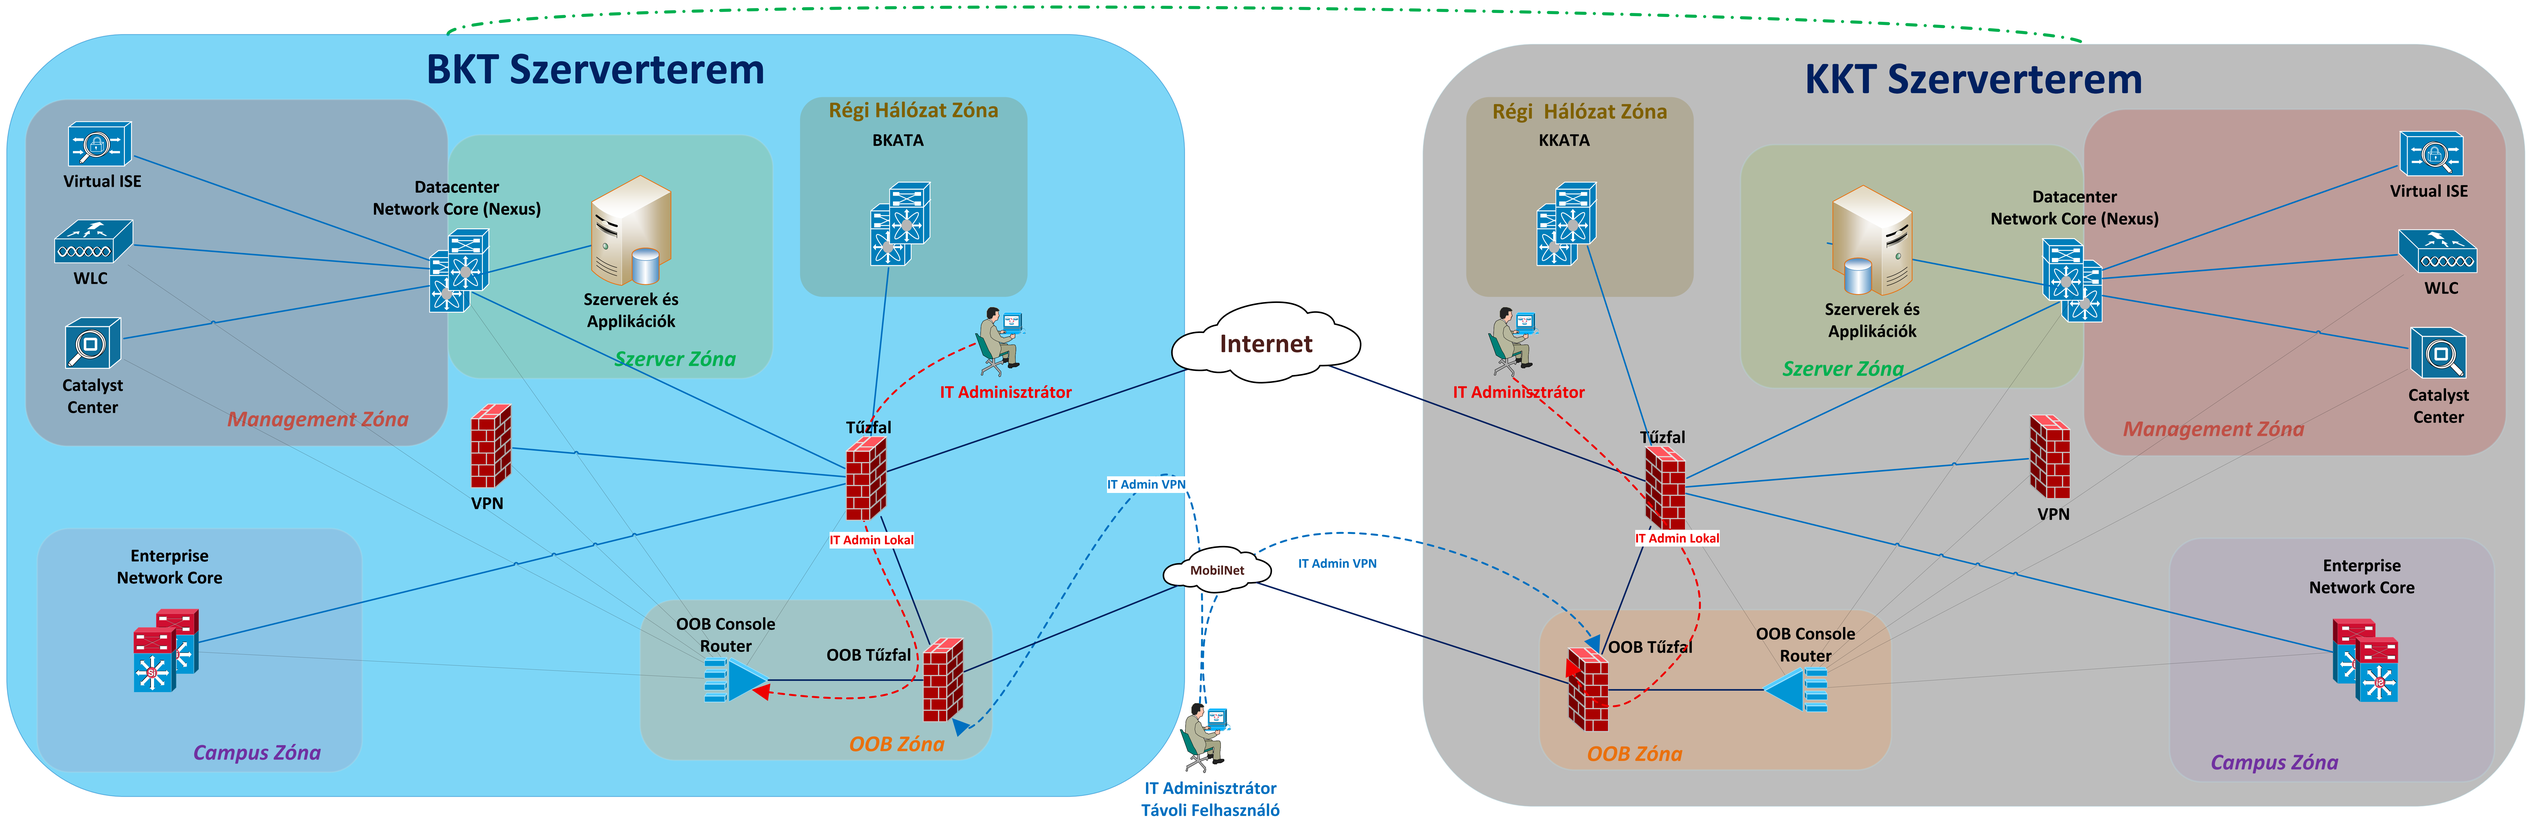
BKT Szerverterem
Virtual ISE
WLC
Catalyst Center
Management Zóna
Datacenter Network Core (Nexus)
Szerverek és Applikációk
Szerver Zóna
Régi Hálózat Zóna
BKATA
IT Adminisztrátor
Internet
Tűzfal
VPN
IT Admin Lokal
IT Admin VPN
Enterprise Network Core
Campus Zóna
OOB Console Router
OOB Tűzfal
OOB Zóna
MobilNet
IT Adminisztrátor Távoli Felhasználó
KKT Szerverterem
Régi Hálózat Zóna
KKATA
IT Adminisztrátor
Szerverek és Applikációk
Szerver Zóna
Datacenter Network Core (Nexus)
Virtual ISE
WLC
Catalyst Center
Management Zóna
Tűzfal
IT Admin Lokal
VPN
IT Admin VPN
OOB Tűzfal
OOB Console Router
OOB Zóna
Enterprise Network Core
Campus Zóna

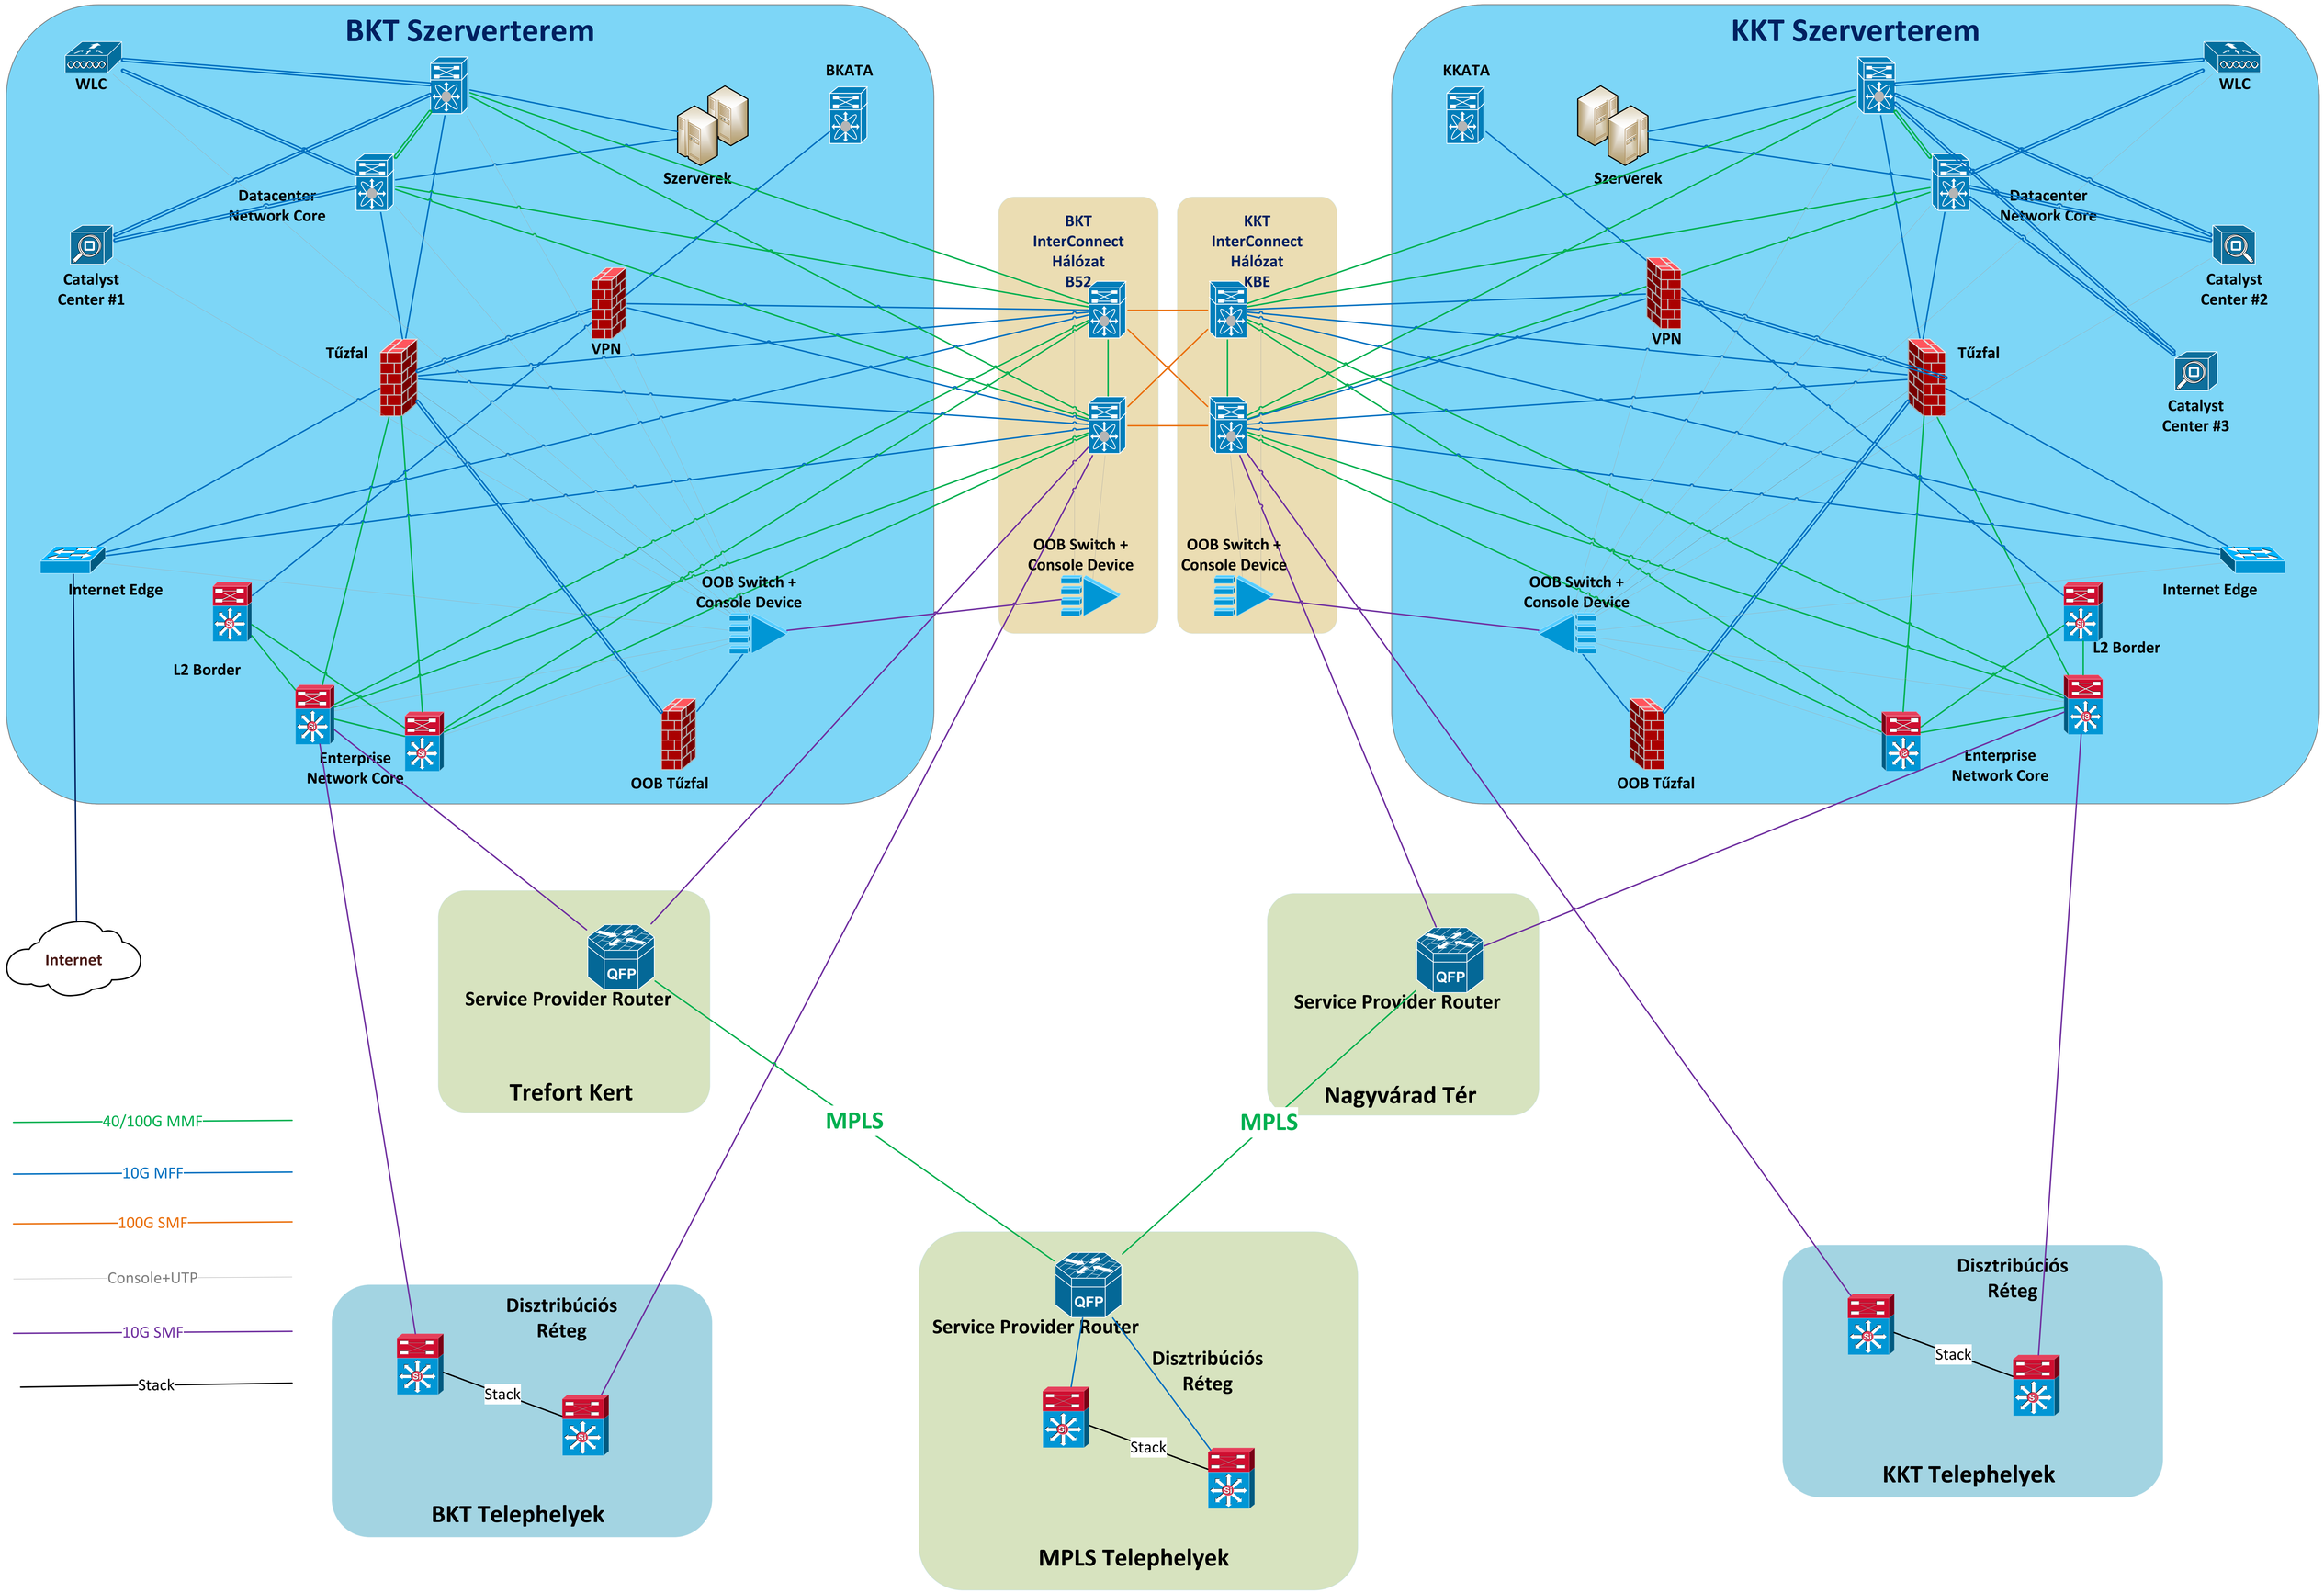
BKT Szerverterem
WLC
BKATA
Szerverek
Datacenter Network Core
Catalyst Center #1
VPN
Tűzfal
Internet Edge
L2 Border
OOB Switch + Console Device
Enterprise Network Core
OOB Tűzfal
BKT InterConnect Hálózat B52
KKT InterConnect Hálózat KBE
OOB Switch + Console Device
OOB Switch + Console Device
KKT Szerverterem
KKATA
Szerverek
WLC
Datacenter Network Core
Catalyst Center #2
VPN
Tűzfal
Catalyst Center #3
Internet Edge
OOB Switch + Console Device
L2 Border
OOB Tűzfal
Enterprise Network Core
Internet
QFP
Service Provider Router
Trefort Kert
MPLS
QFP
Service Provider Router
Nagyvárad Tér
MPLS
40/100G MMF
10G MFF
100G SMF
Console+UTP
10G SMF
Stack
Disztribúciós Réteg
Stack
BKT Telephelyek
QFP
Service Provider Router
Disztribúciós Réteg
Stack
MPLS Telephelyek
Disztribúciós Réteg
Stack
KKT Telephelyek

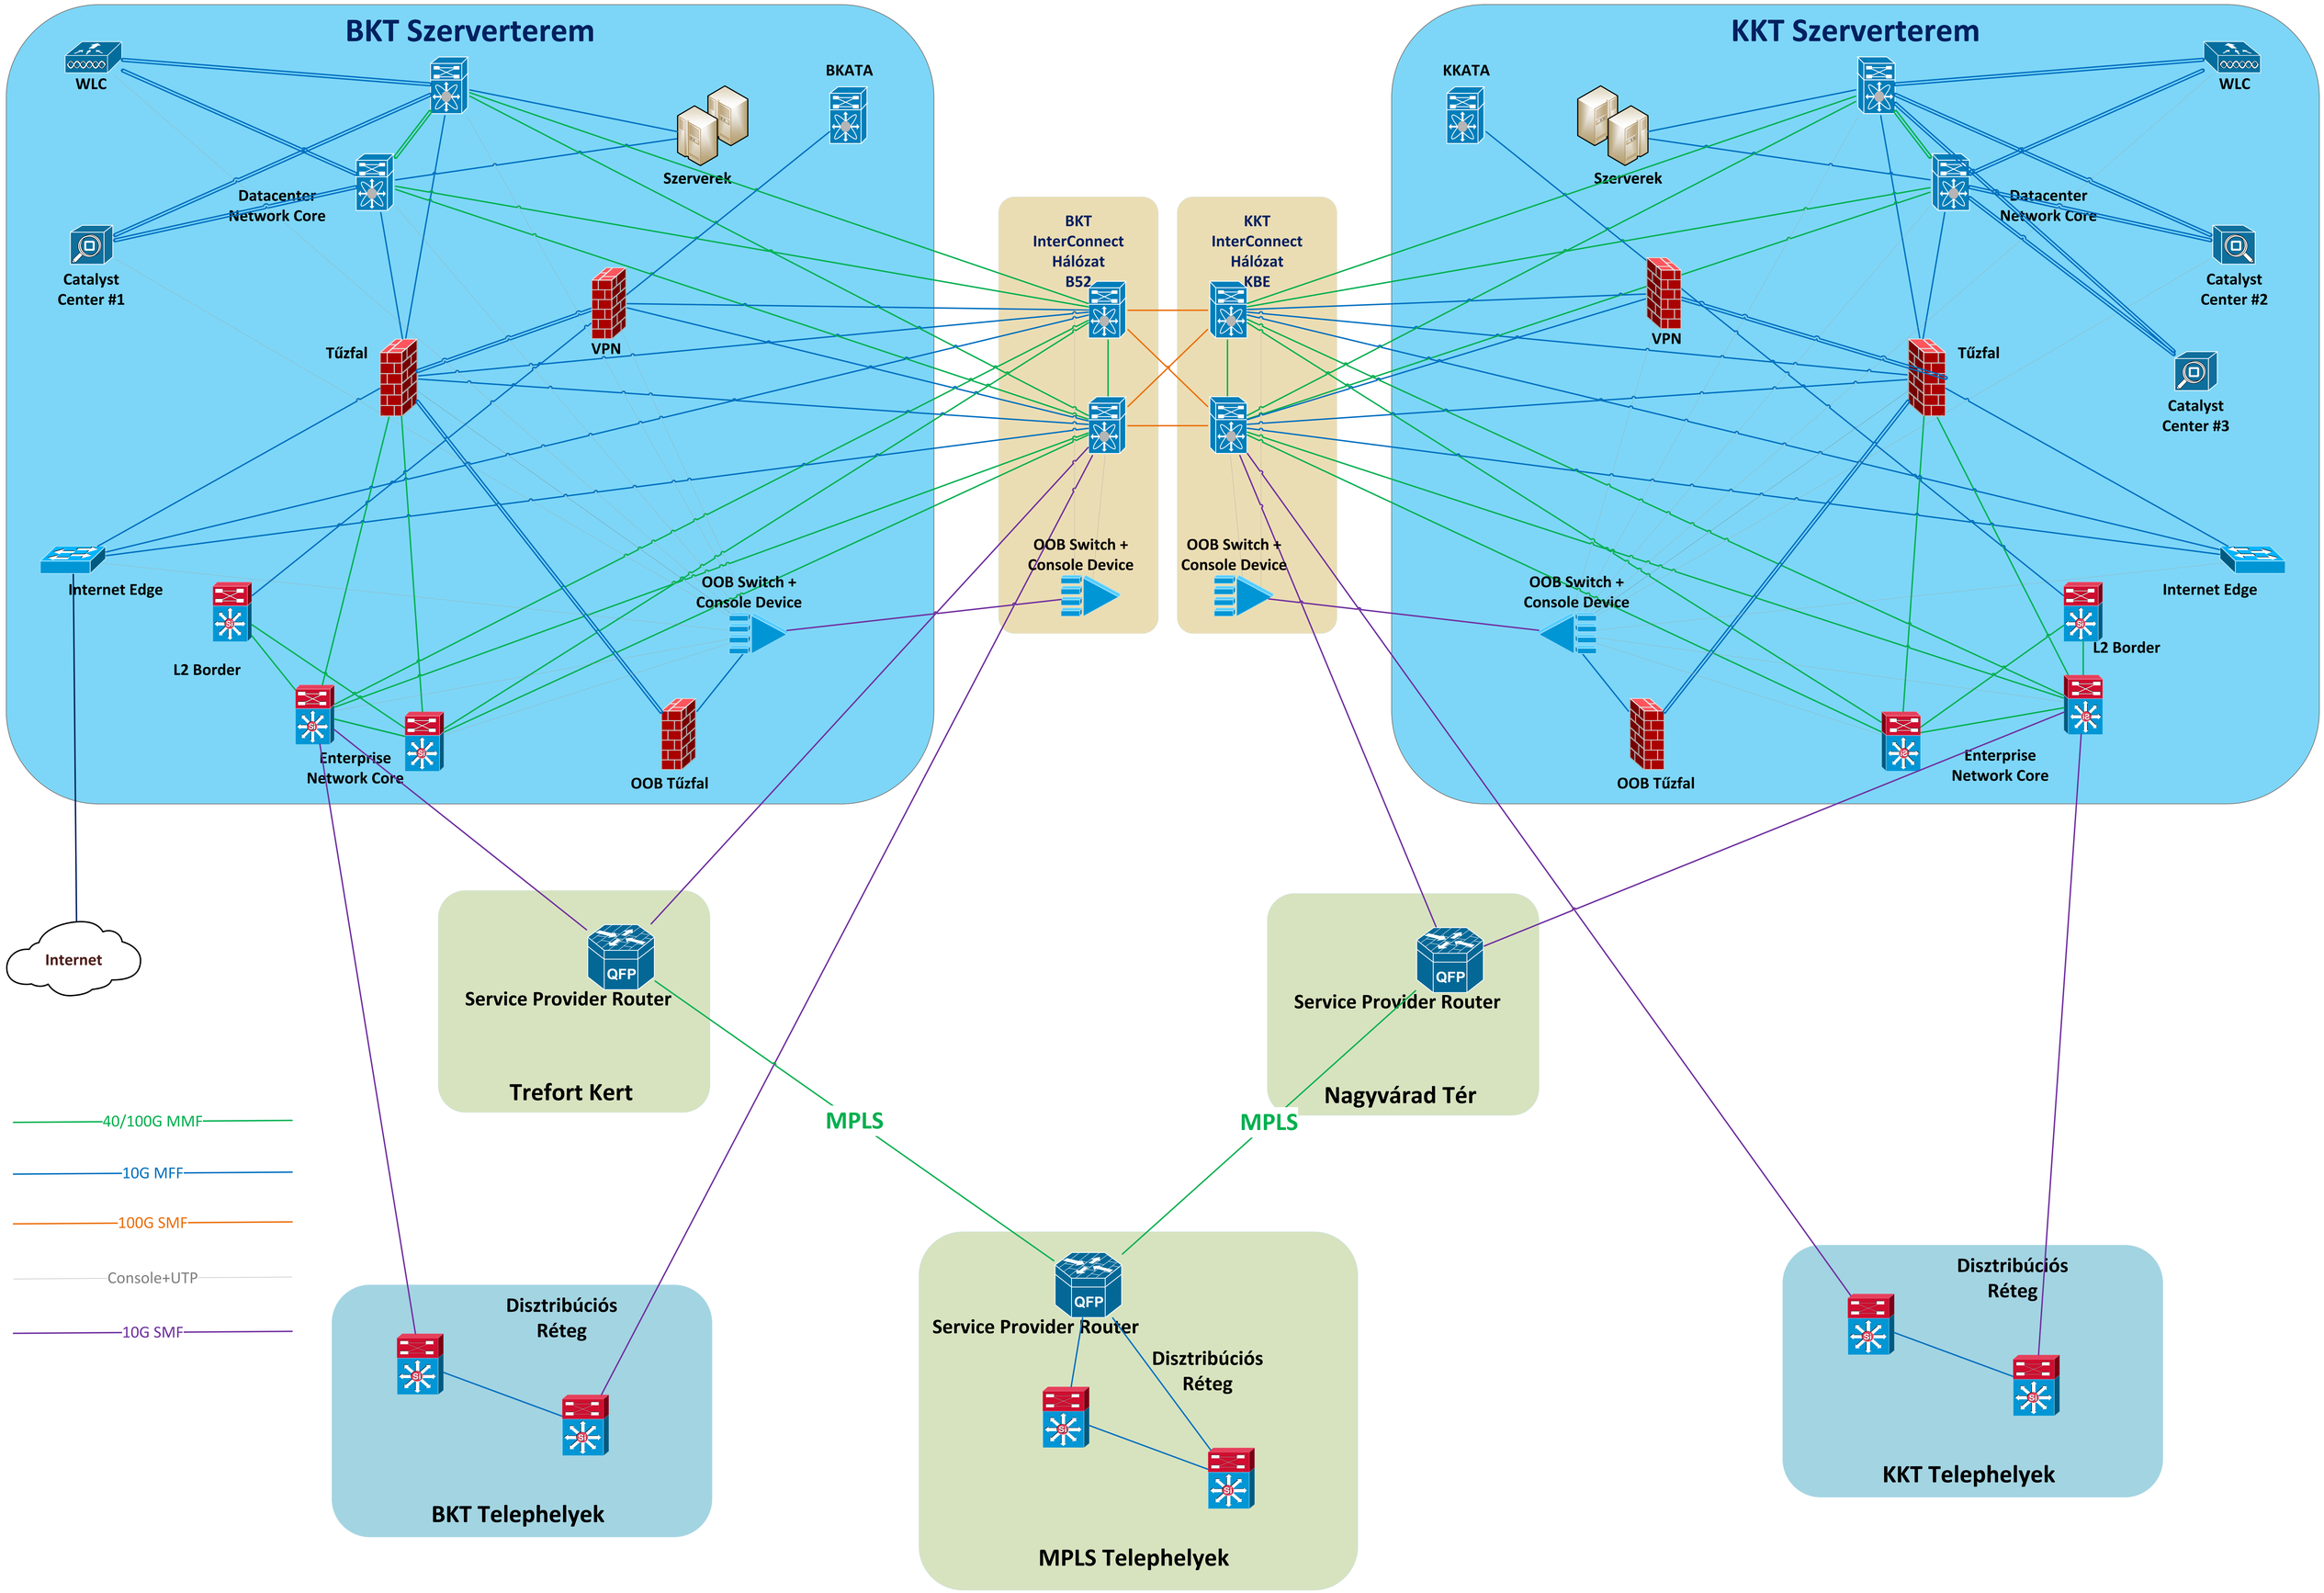
BKT Szerverterem
WLC
BKATA
Szerverek
Datacenter Network Core
Catalyst Center #1
VPN
Tűzfal
Internet Edge
L2 Border
OOB Switch + Console Device
Enterprise Network Core
OOB Tűzfal
BKT InterConnect Hálózat B52
KKT InterConnect Hálózat KBE
OOB Switch + Console Device
OOB Switch + Console Device
KKT Szerverterem
KKATA
Szerverek
WLC
Datacenter Network Core
Catalyst Center #2
VPN
Tűzfal
Catalyst Center #3
Internet Edge
OOB Switch + Console Device
L2 Border
OOB Tűzfal
Enterprise Network Core
Internet
QFP
Service Provider Router
Trefort Kert
MPLS
QFP
Service Provider Router
Nagyvárad Tér
MPLS
40/100G MMF
10G MFF
100G SMF
Console+UTP
10G SMF
Disztribúciós Réteg
BKT Telephelyek
QFP
Service Provider Router
Disztribúciós Réteg
MPLS Telephelyek
Disztribúciós Réteg
KKT Telephelyek

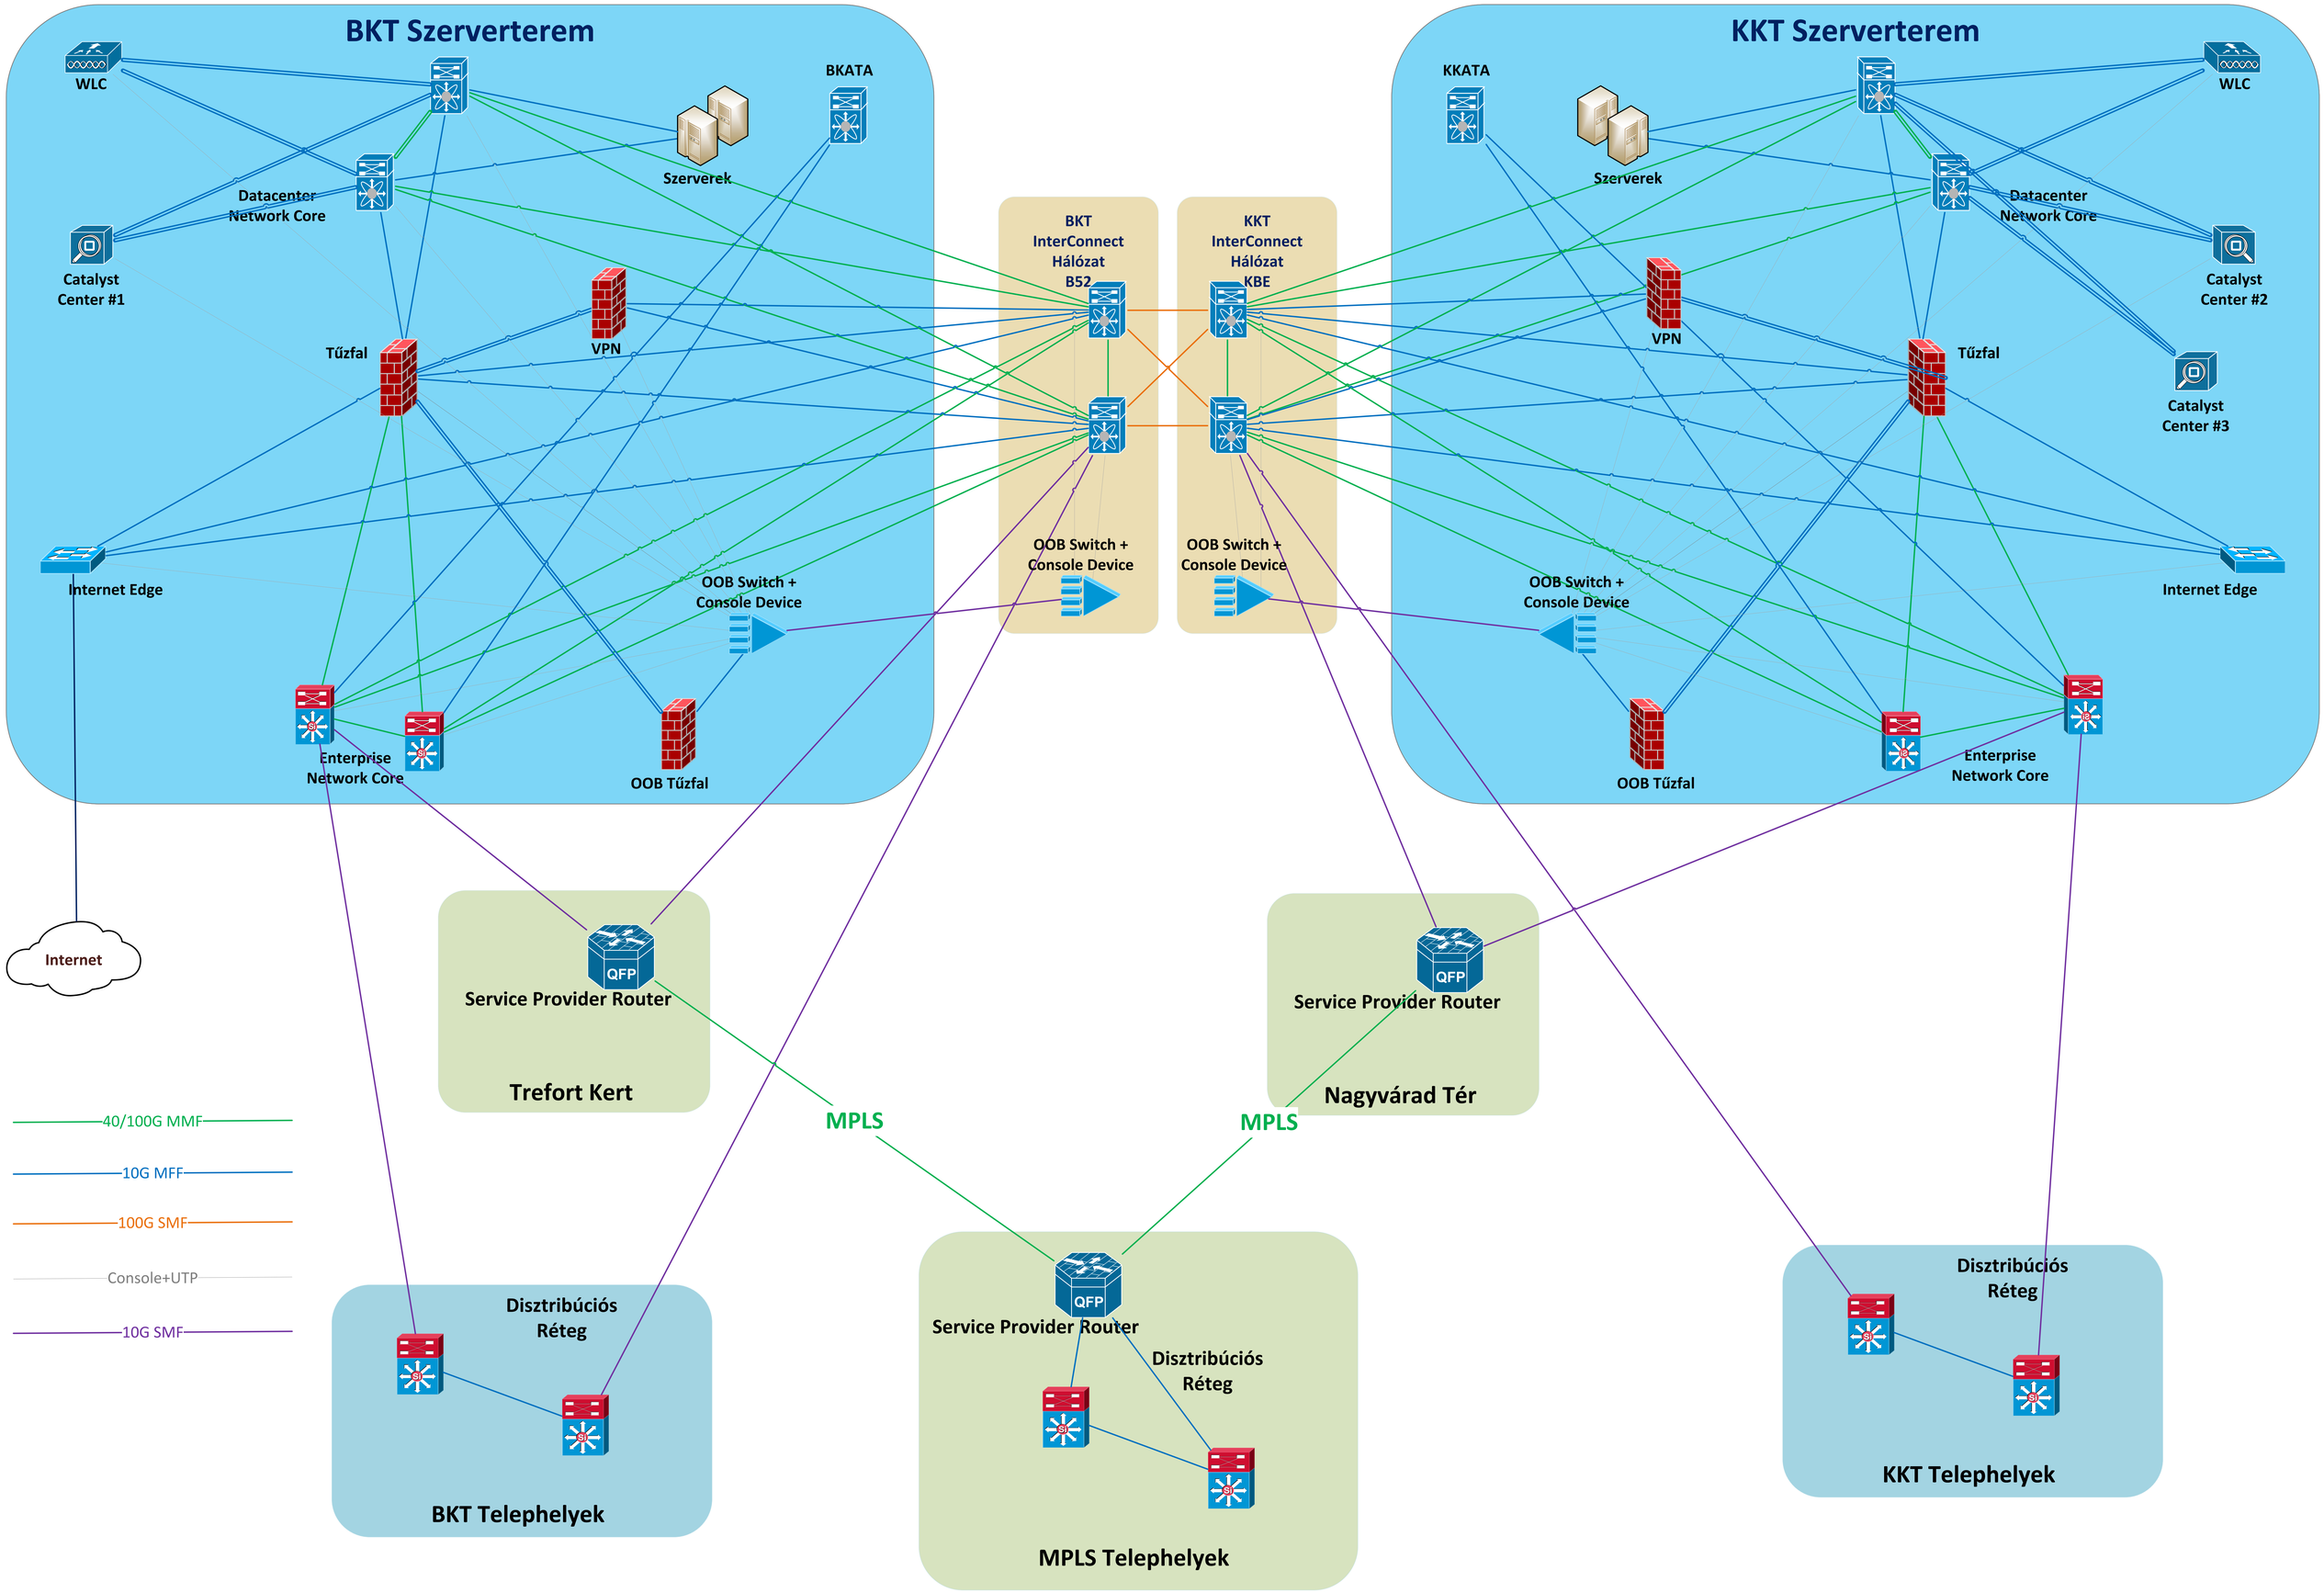
BKT Szerverterem
WLC
BKATA
Szerverek
Datacenter Network Core
Catalyst Center #1
VPN
Tűzfal
Internet Edge
OOB Switch + Console Device
Enterprise Network Core
OOB Tűzfal
BKT InterConnect Hálózat B52
KKT InterConnect Hálózat KBE
OOB Switch + Console Device
OOB Switch + Console Device
KKT Szerverterem
KKATA
Szerverek
WLC
Datacenter Network Core
Catalyst Center #2
Catalyst Center #3
VPN
Tűzfal
Internet Edge
OOB Switch + Console Device
OOB Tűzfal
Enterprise Network Core
Internet
QFP
Service Provider Router
Trefort Kert
MPLS
QFP
Service Provider Router
Nagyvárad Tér
MPLS
40/100G MMF
10G MFF
100G SMF
Console+UTP
10G SMF
Disztribúciós Réteg
BKT Telephelyek
QFP
Service Provider Router
Disztribúciós Réteg
MPLS Telephelyek
Disztribúciós Réteg
KKT Telephelyek

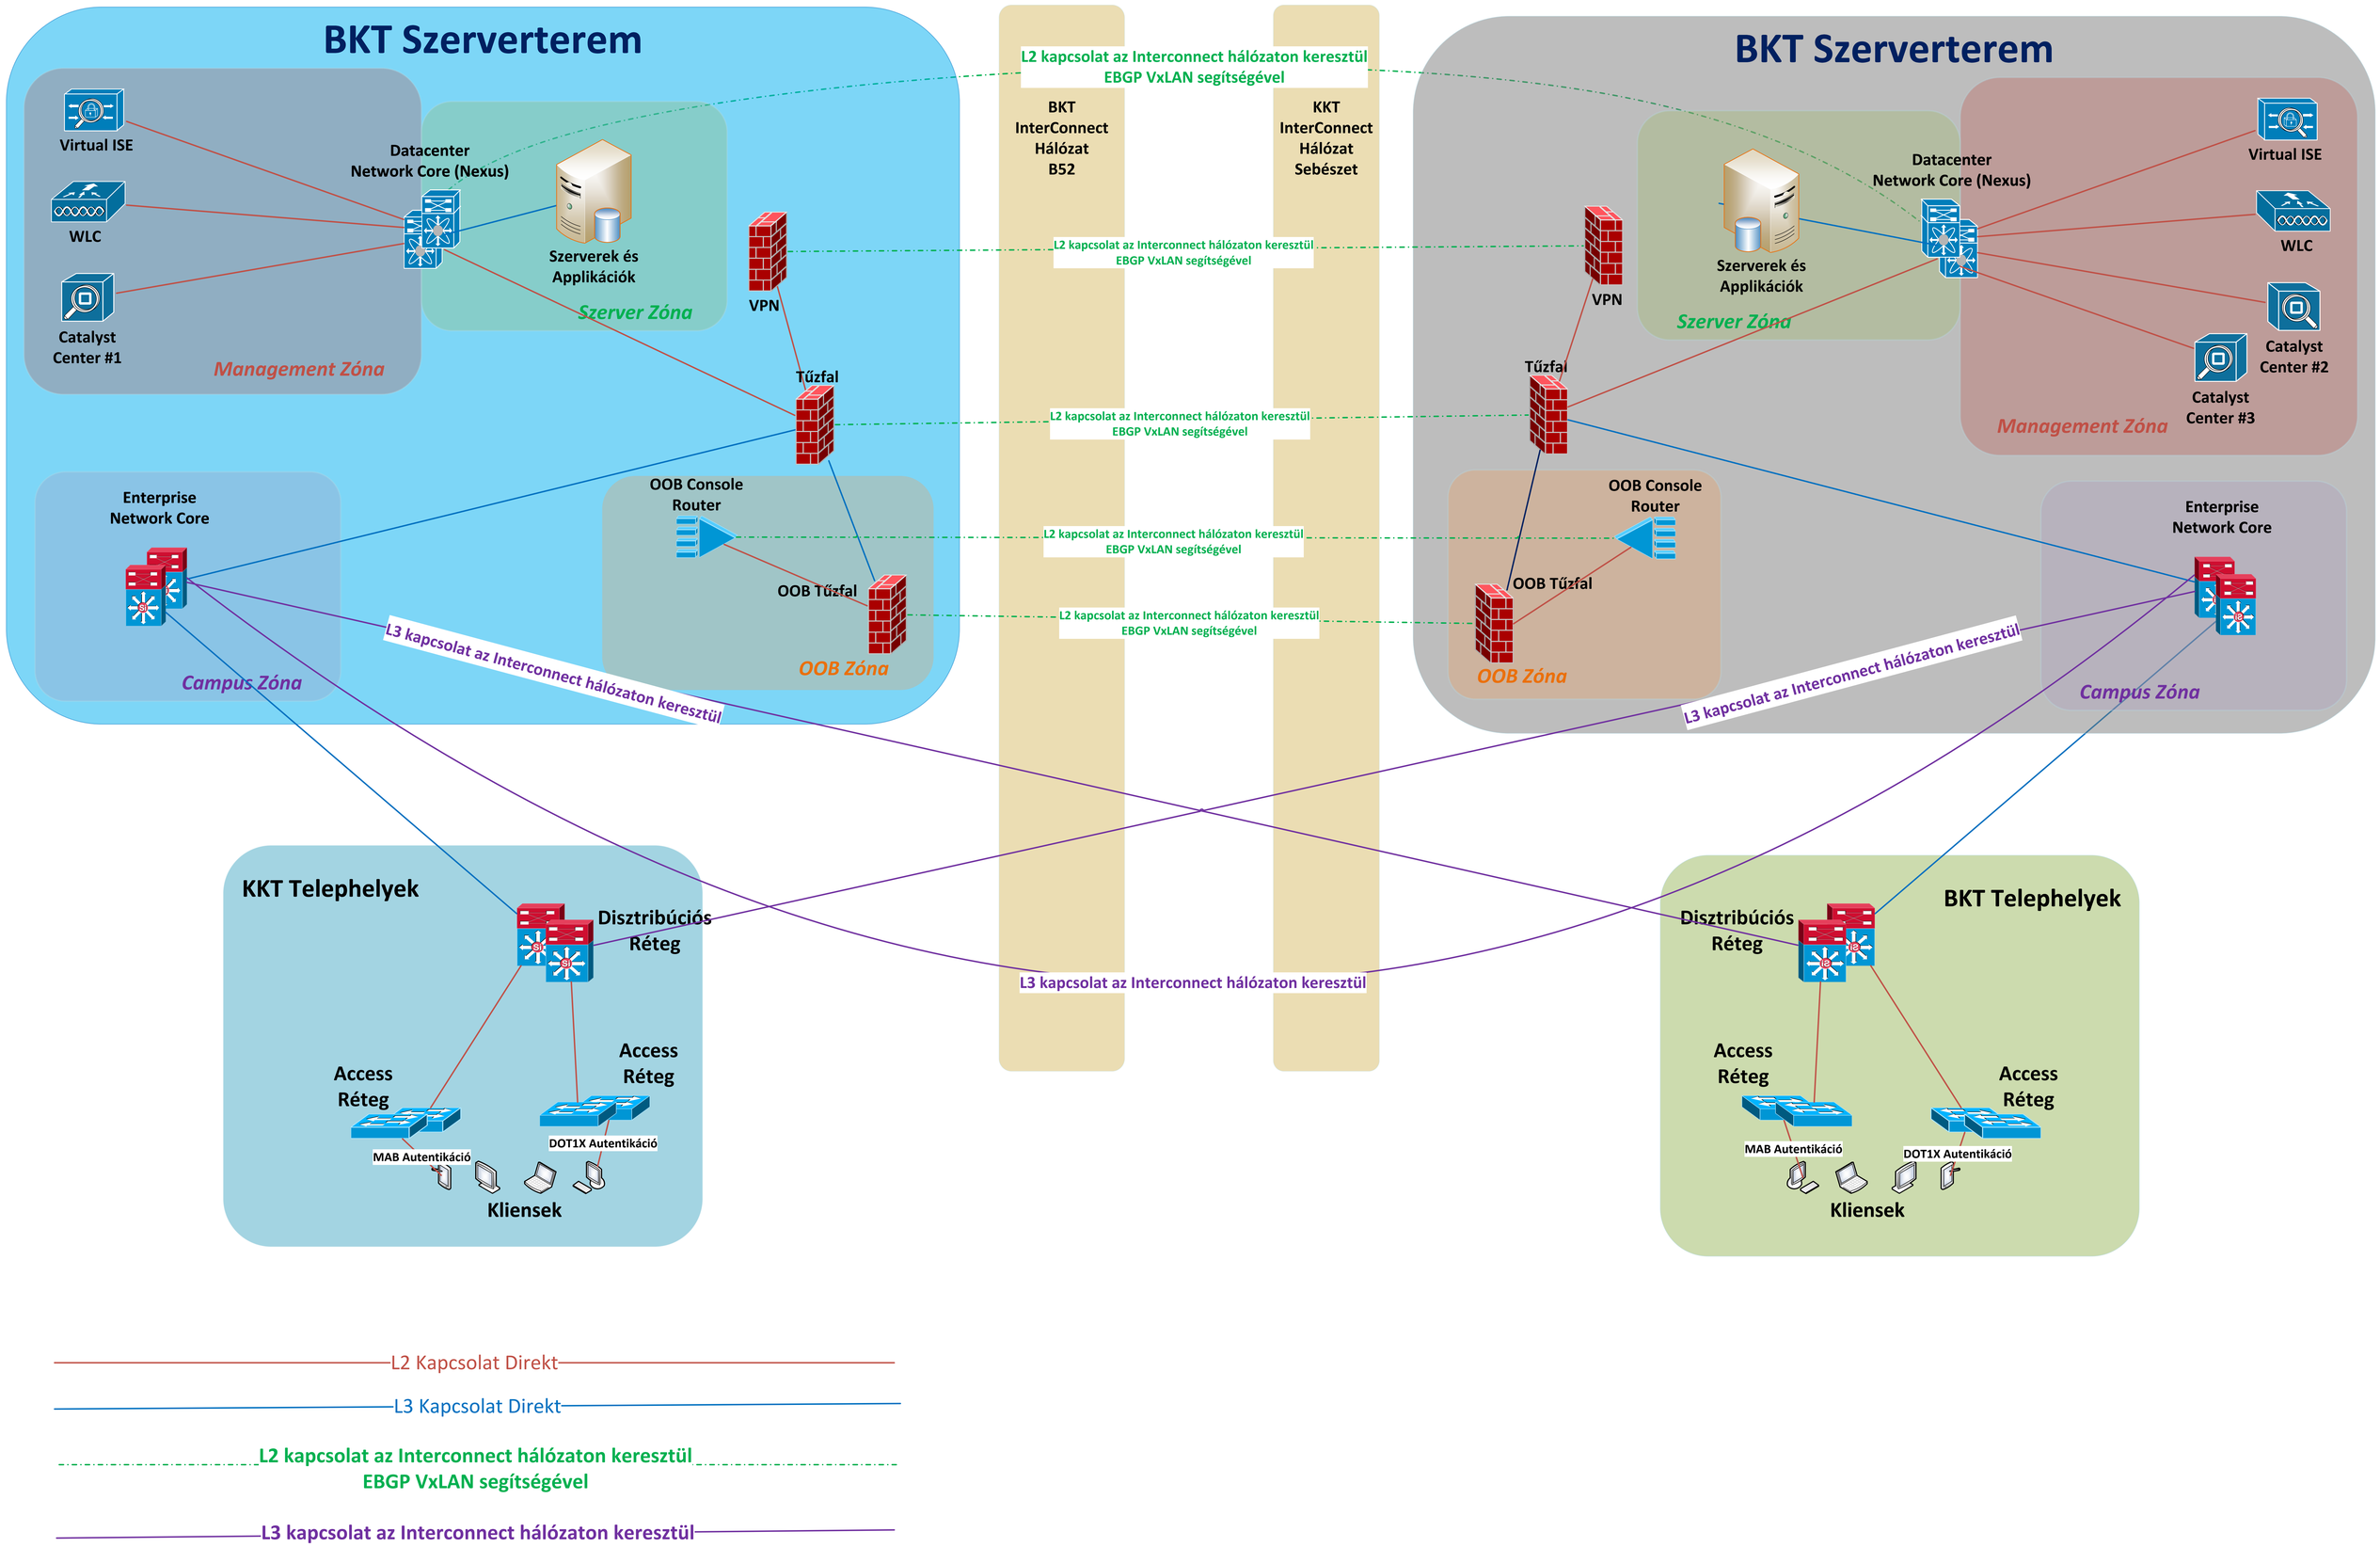
BKT Szerverterem
Virtual ISE
WLC
Catalyst Center #1
Management Zóna
Datacenter Network Core (Nexus)
Szerverek és Applikációk
Szerver Zóna
VPN
Tűzfal
Enterprise Network Core
Campus Zóna
OOB Console Router
OOB Tűzfal
OOB Zóna
L3 kapcsolat az Interconnect hálózaton keresztül
L2 kapcsolat az Interconnect hálózaton keresztül EBGP VxLAN segítségével
BKT InterConnect Hálózat B52
KKT InterConnect Hálózat Sebészet
BKT Szerverterem
Virtual ISE
WLC
Catalyst Center #2
Catalyst Center #3
Management Zóna
Datacenter Network Core (Nexus)
Szerverek és Applikációk
Szerver Zóna
VPN
Tűzfal
OOB Console Router
OOB Tűzfal
OOB Zóna
Enterprise Network Core
Campus Zóna
L3 kapcsolat az Interconnect hálózaton keresztül
KKT Telephelyek
Disztribúciós Réteg
Access Réteg
Access Réteg
MAB Autentikáció
DOT1X Autentikáció
Kliensek
BKT Telephelyek
Disztribúciós Réteg
Access Réteg
Access Réteg
MAB Autentikáció
DOT1X Autentikáció
Kliensek
L2 Kapcsolat Direkt
L3 Kapcsolat Direkt
L2 kapcsolat az Interconnect hálózaton keresztül EBGP VxLAN segítségével
L3 kapcsolat az Interconnect hálózaton keresztül

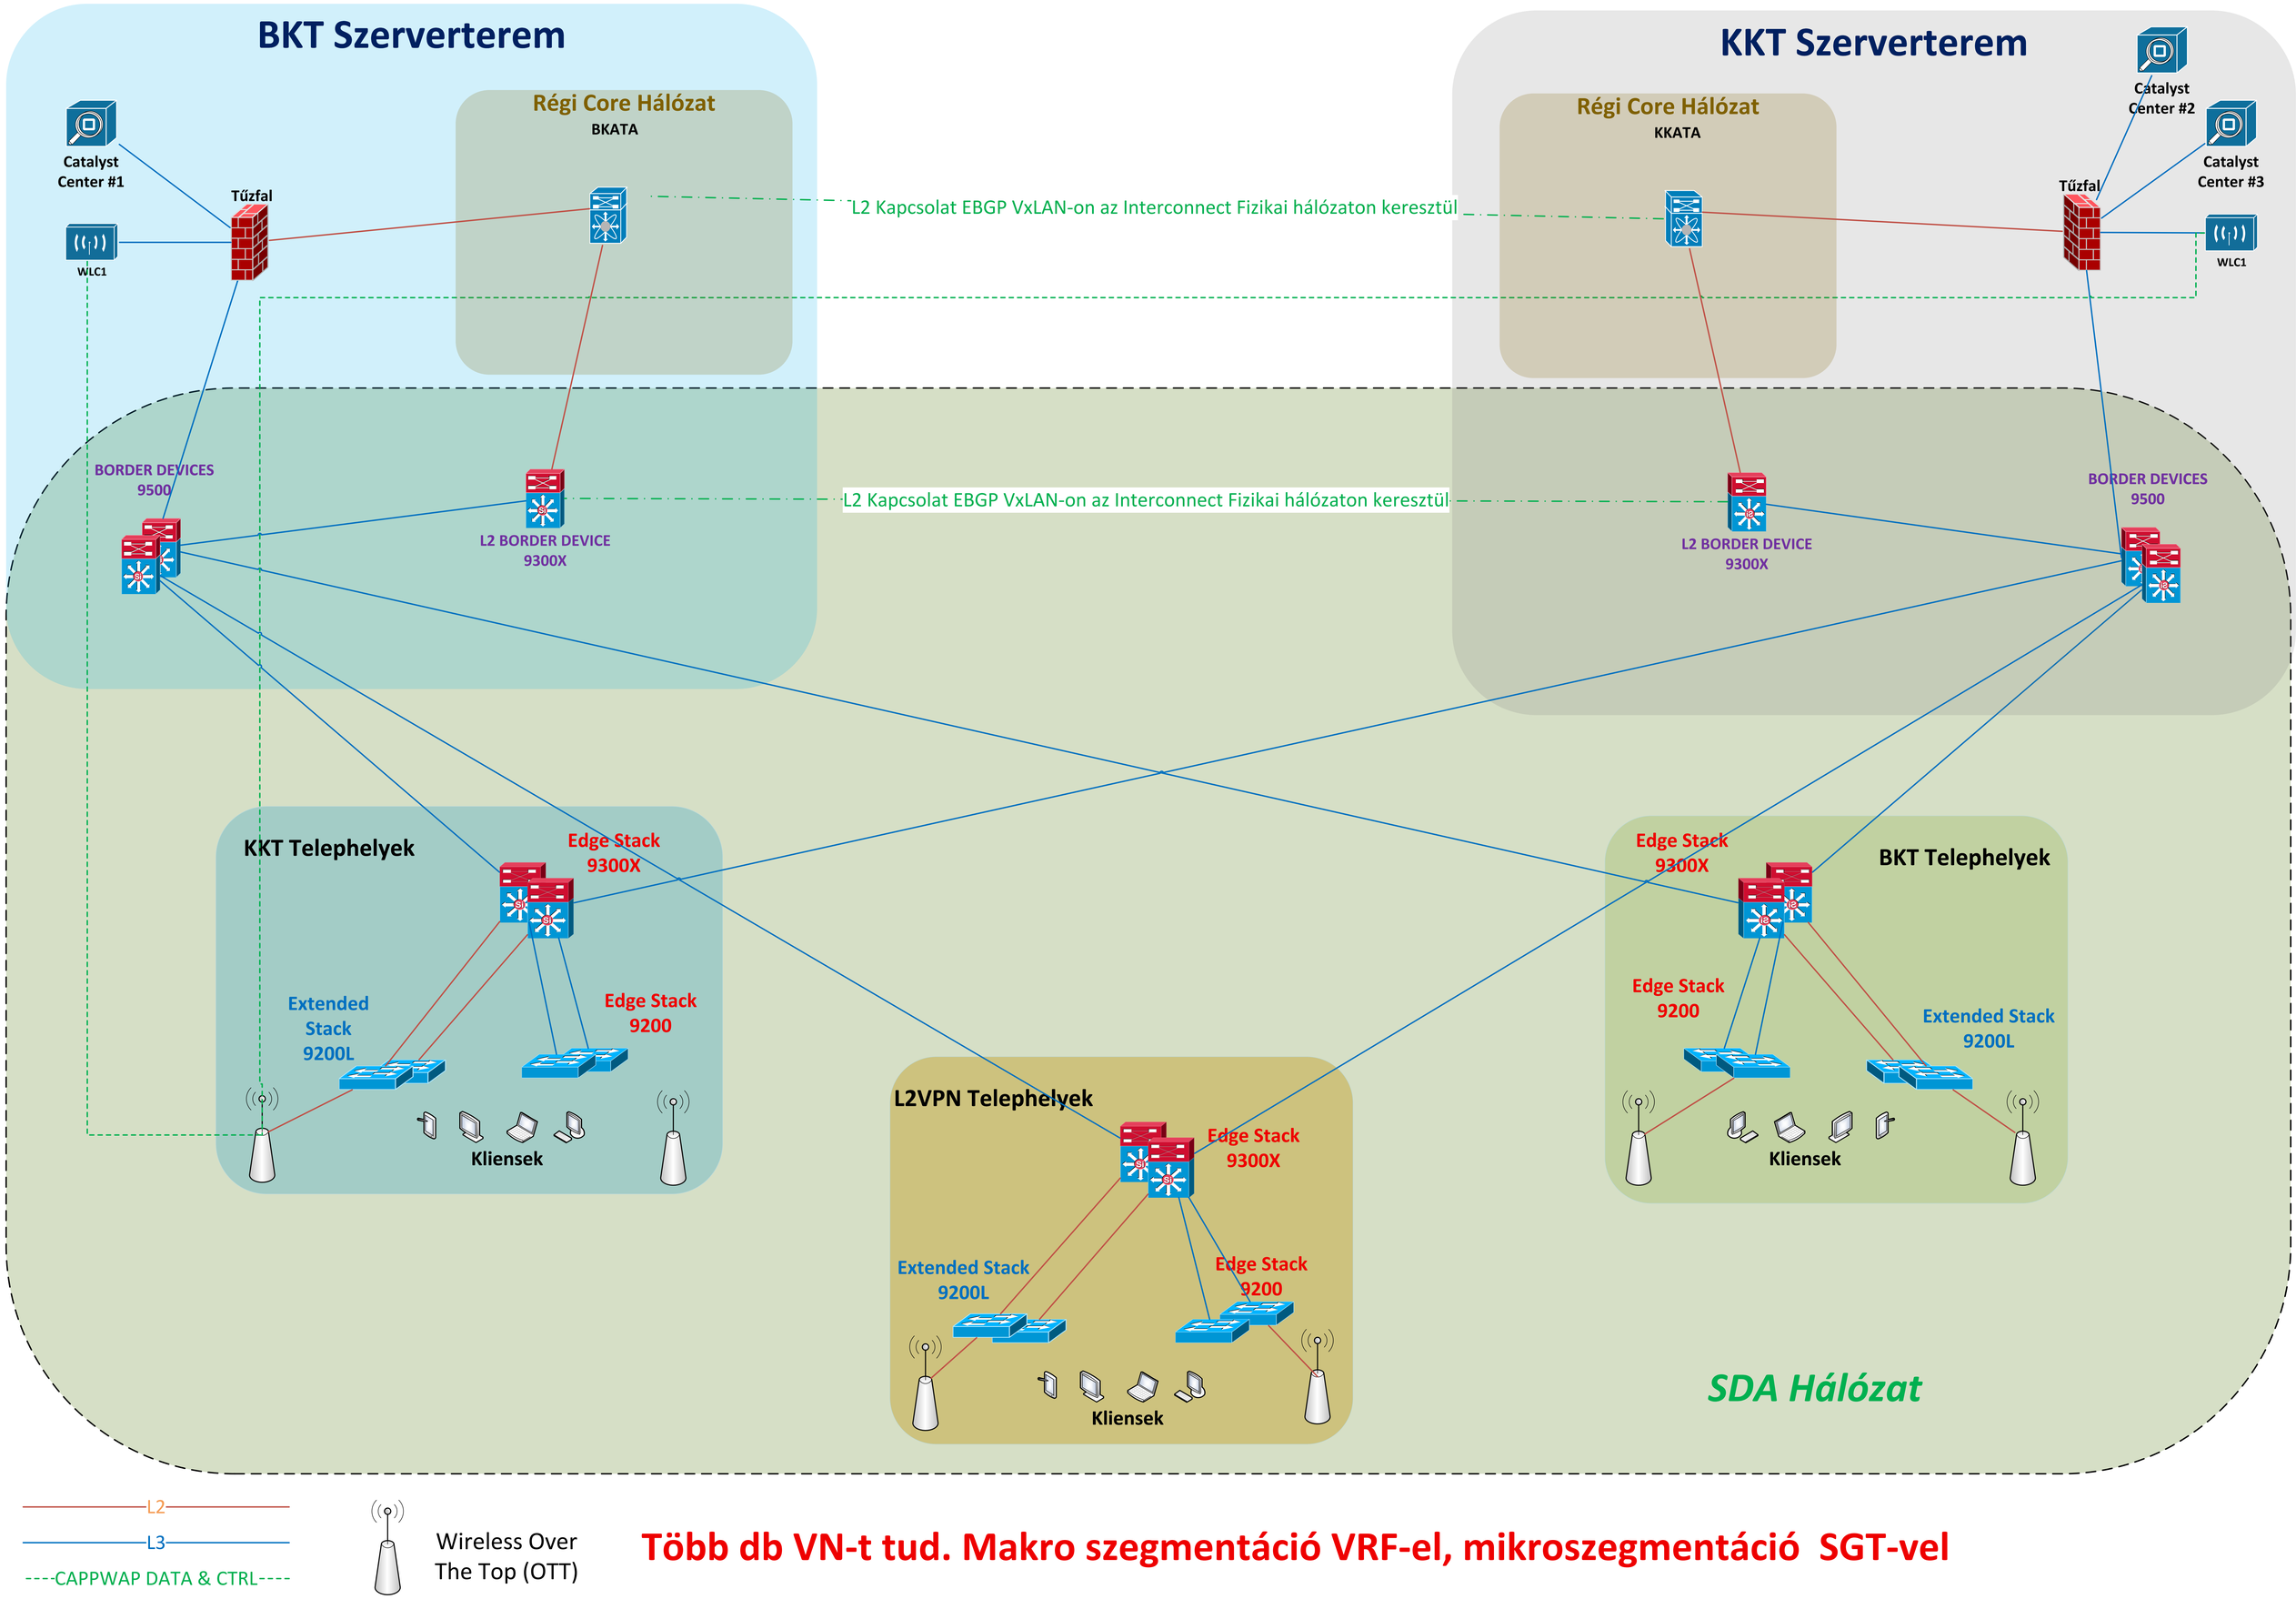

Több db VN-t tud. Makro szegmentáció VRF-el, mikroszegmentáció SGT-vel

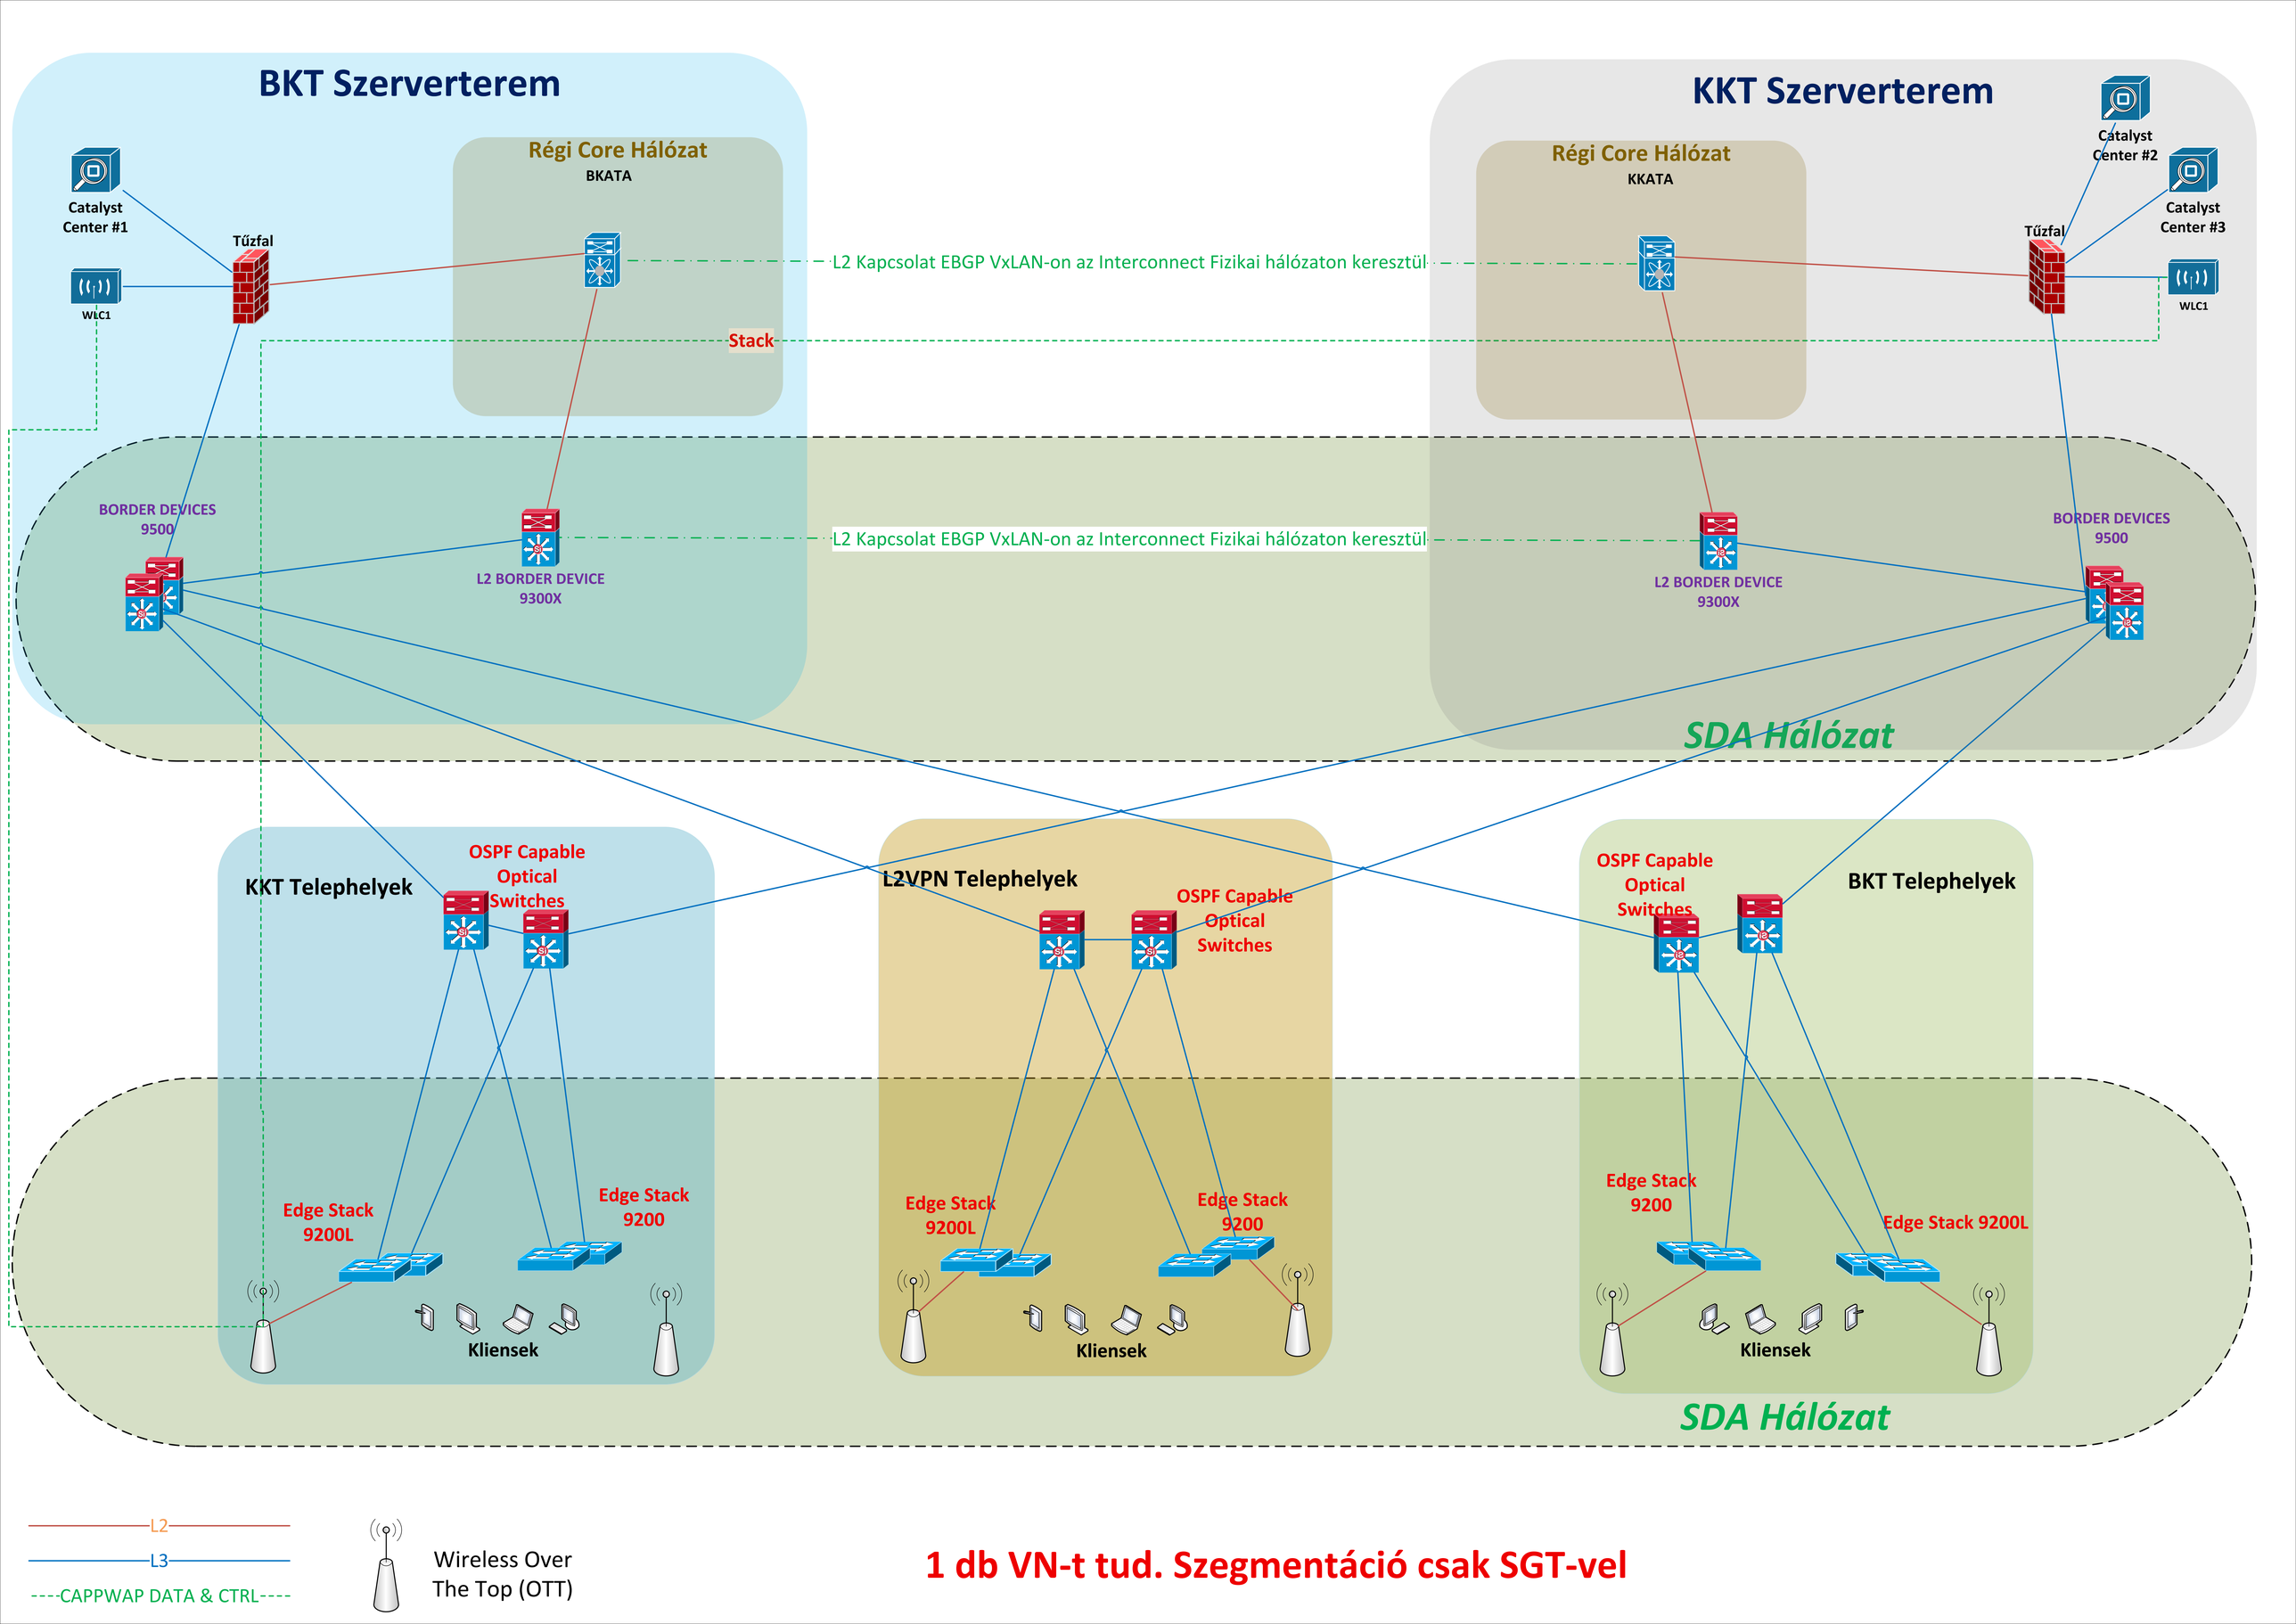
BKT Szerverterem
KKT Szerverterem
Régi Core Hálózat
BKATA
Régi Core Hálózat
KKATA
Catalyst Center #1
Catalyst Center #2
Catalyst Center #3
Tűzfal
Tűzfal
WLC1
WLC1
L2 Kapcsolat EBGP VxLAN-on az Interconnect Fizikai hálózaton keresztül
Stack
BORDER DEVICES 9500
L2 BORDER DEVICE 9300X
L2 Kapcsolat EBGP VxLAN-on az Interconnect Fizikai hálózaton keresztül
L2 BORDER DEVICE 9300X
BORDER DEVICES 9500
SDA Hálózat
KKT Telephelyek
OSPF Capable Optical Switches
L2VPN Telephelyek
OSPF Capable Optical Switches
OSPF Capable Optical Switches
BKT Telephelyek
Edge Stack 9200L
Edge Stack 9200
Kliensek
Edge Stack 9200L
Edge Stack 9200
Kliensek
Edge Stack 9200
Edge Stack 9200L
Kliensek
SDA Hálózat
L2
L3
CAPPWAP DATA & CTRL
Wireless Over The Top (OTT)
1 db VN-t tud. Szegmentáció csak SGT-vel

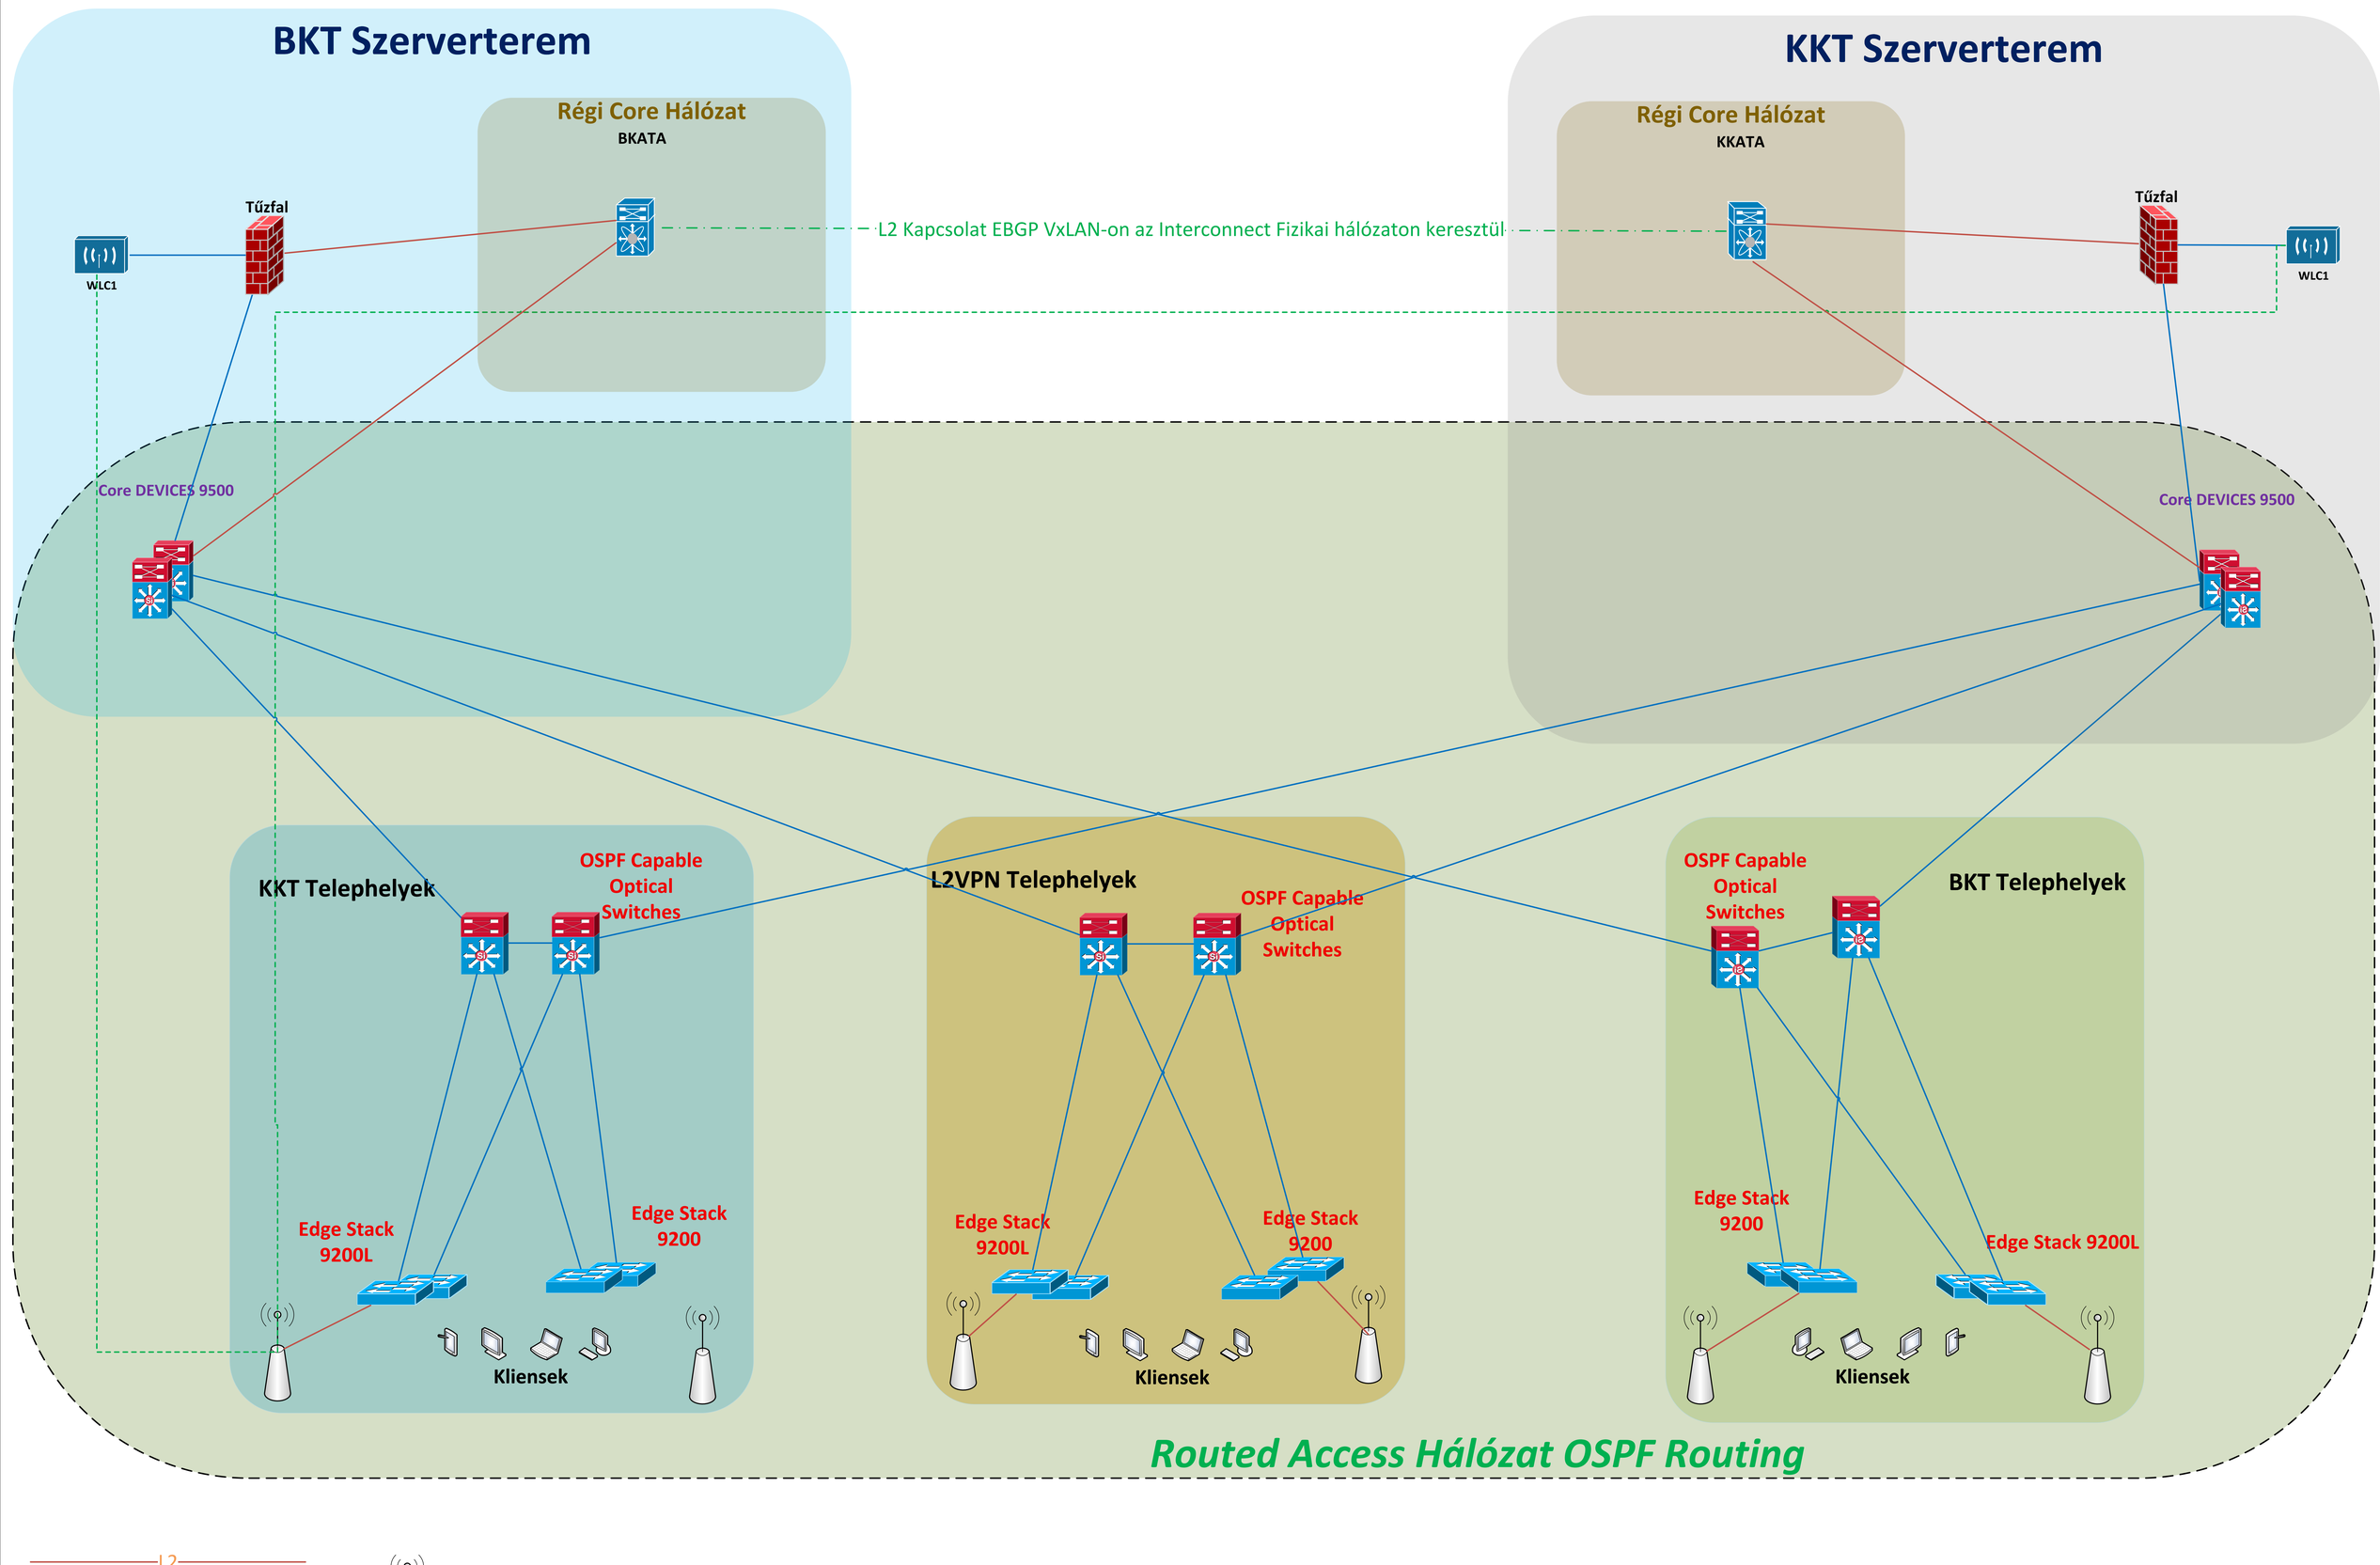

L2

L3

----CAPPWAP DATA & CTRL----

Wireless Marad

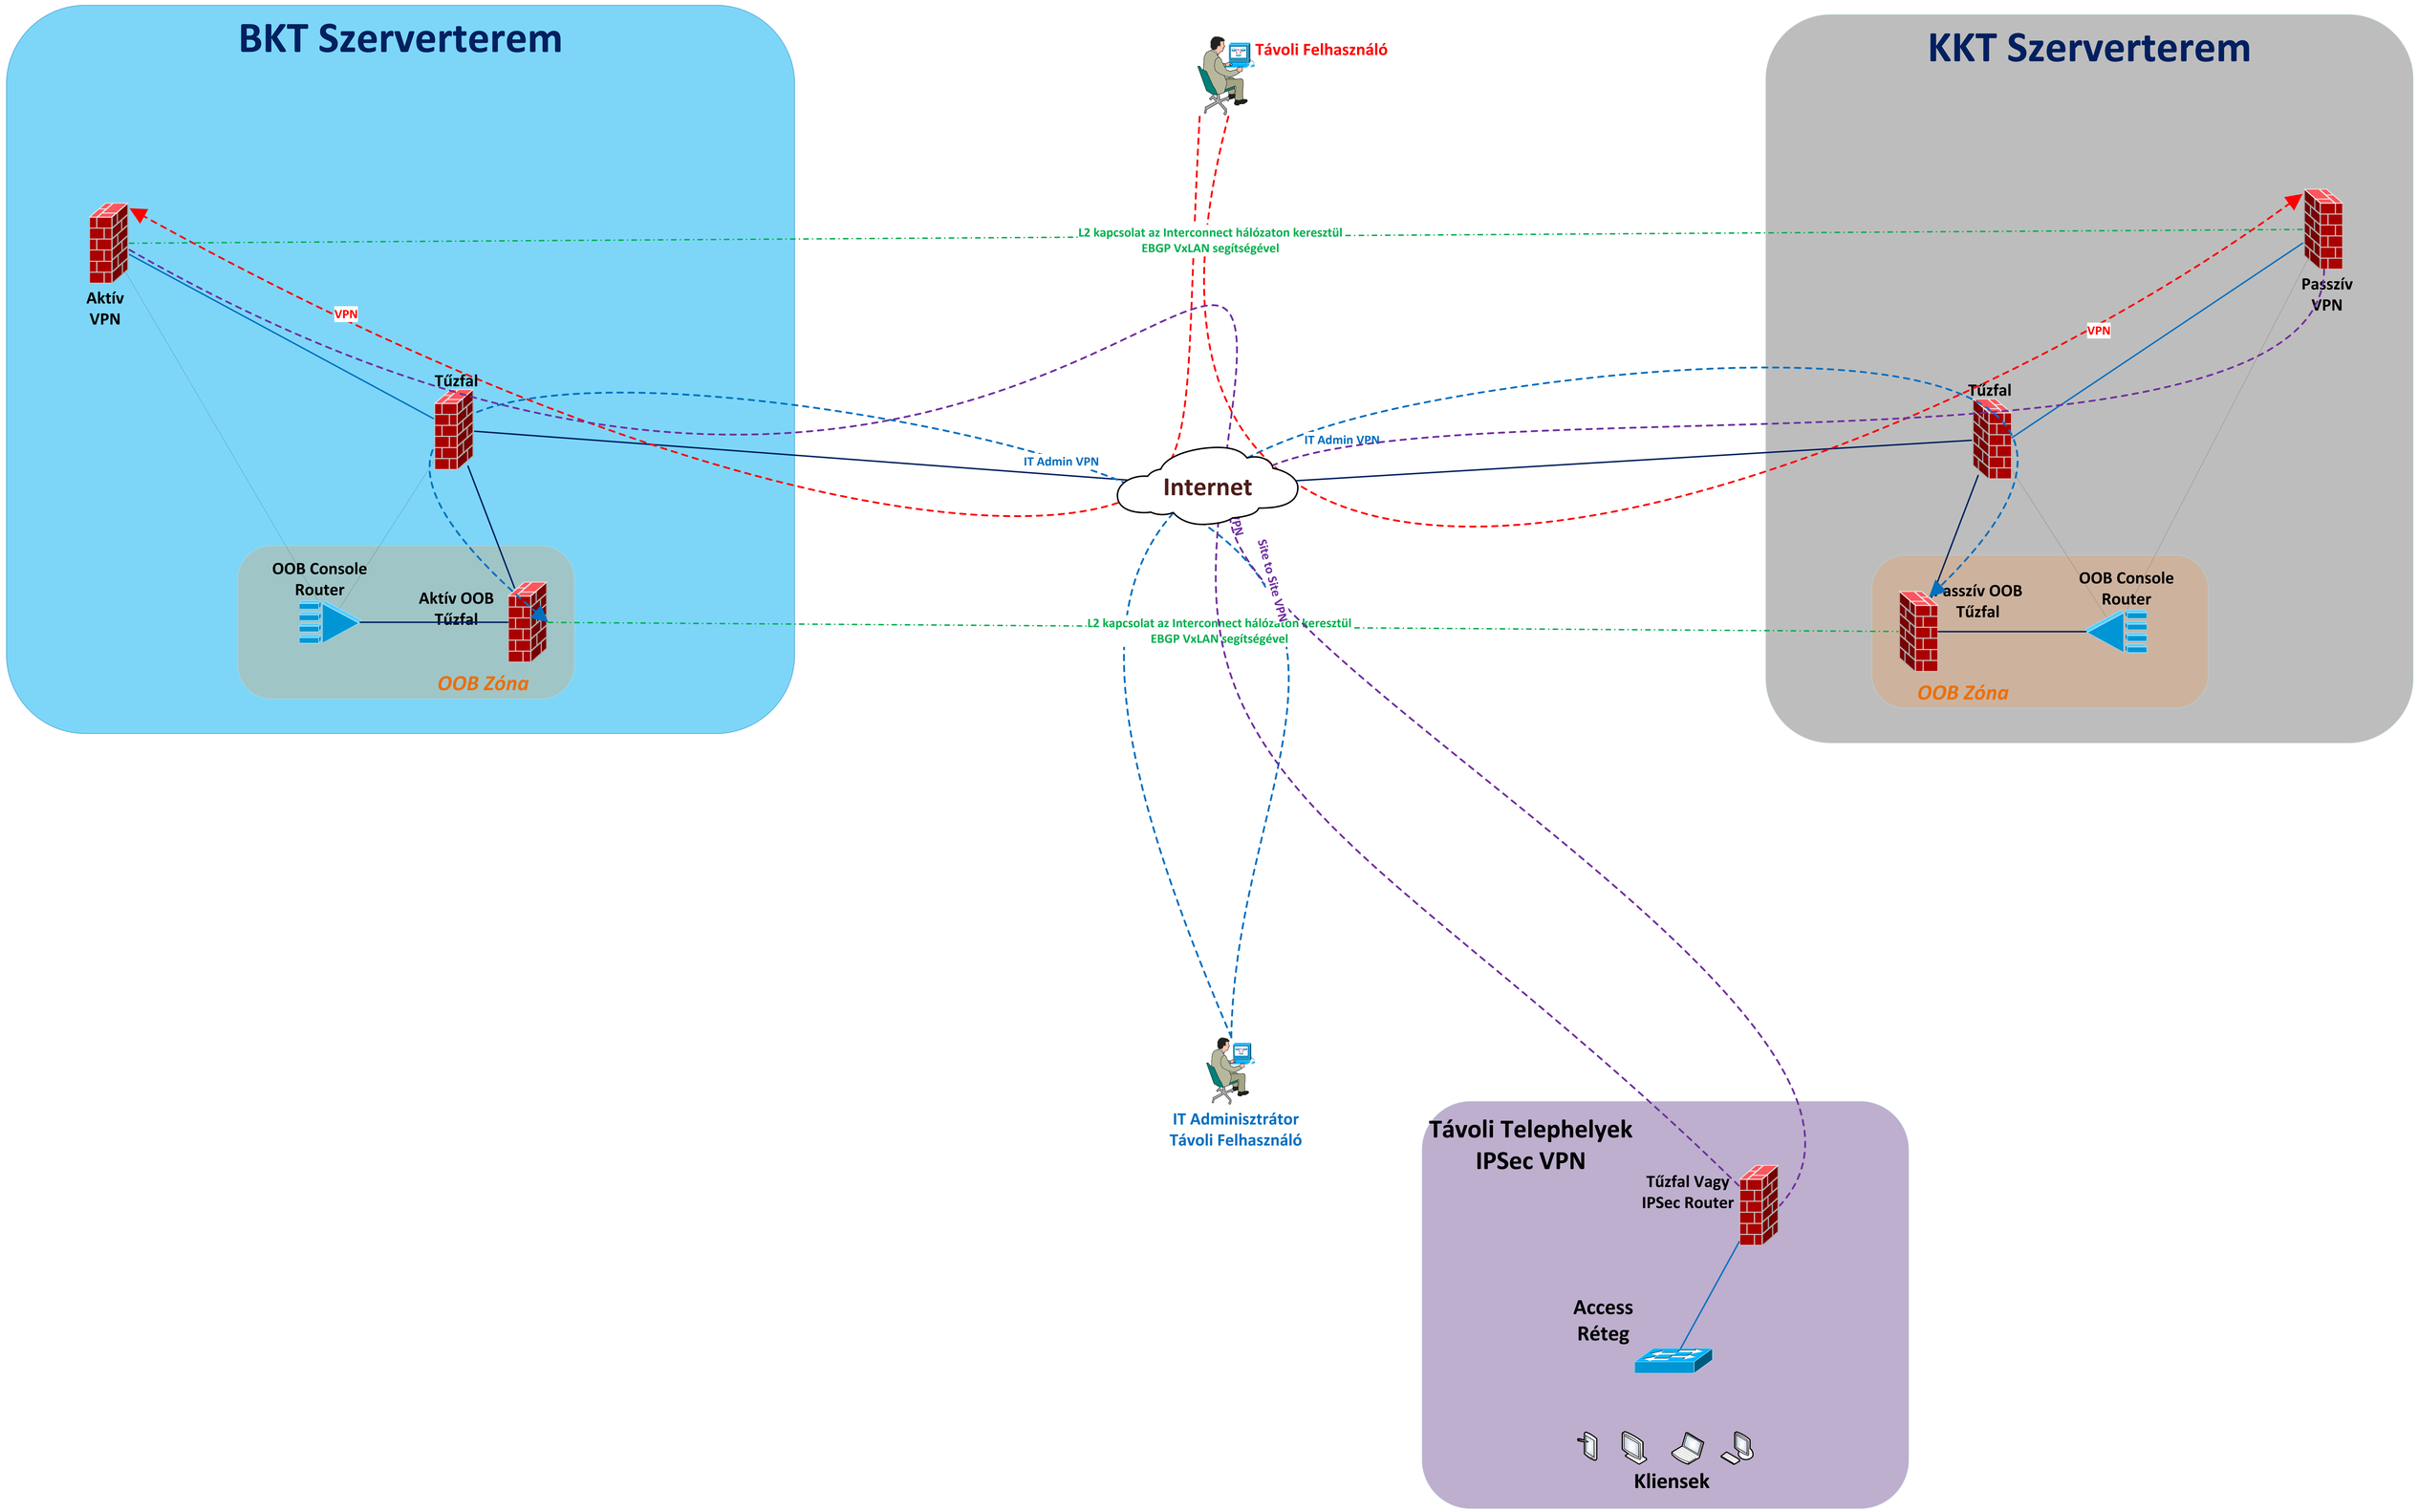
BKT Szerverterem
Távoli Felhasználó
KKT Szerverterem
L2 kapcsolat az Interconnect hálózaton keresztül
EBGP VxLAN segítségével
Aktív
VPN
VPN
Passzív
VPN
VPN
Tűzfal
Tűzfal
IT Admin VPN
IT Admin VPN
Internet
VPN
Site to Site VPN
OOB Console
Router
Aktív OOB
Tűzfal
OOB Zóna
L2 kapcsolat az Interconnect hálózaton keresztül
EBGP VxLAN segítségével
Passzív OOB
Tűzfal
OOB Console
Router
OOB Zóna
IT Adminisztrátor
Távoli Felhasználó
Távoli Telephelyek
IPSec VPN
Tűzfal Vagy
IPSec Router
Access
Réteg
Kliensek

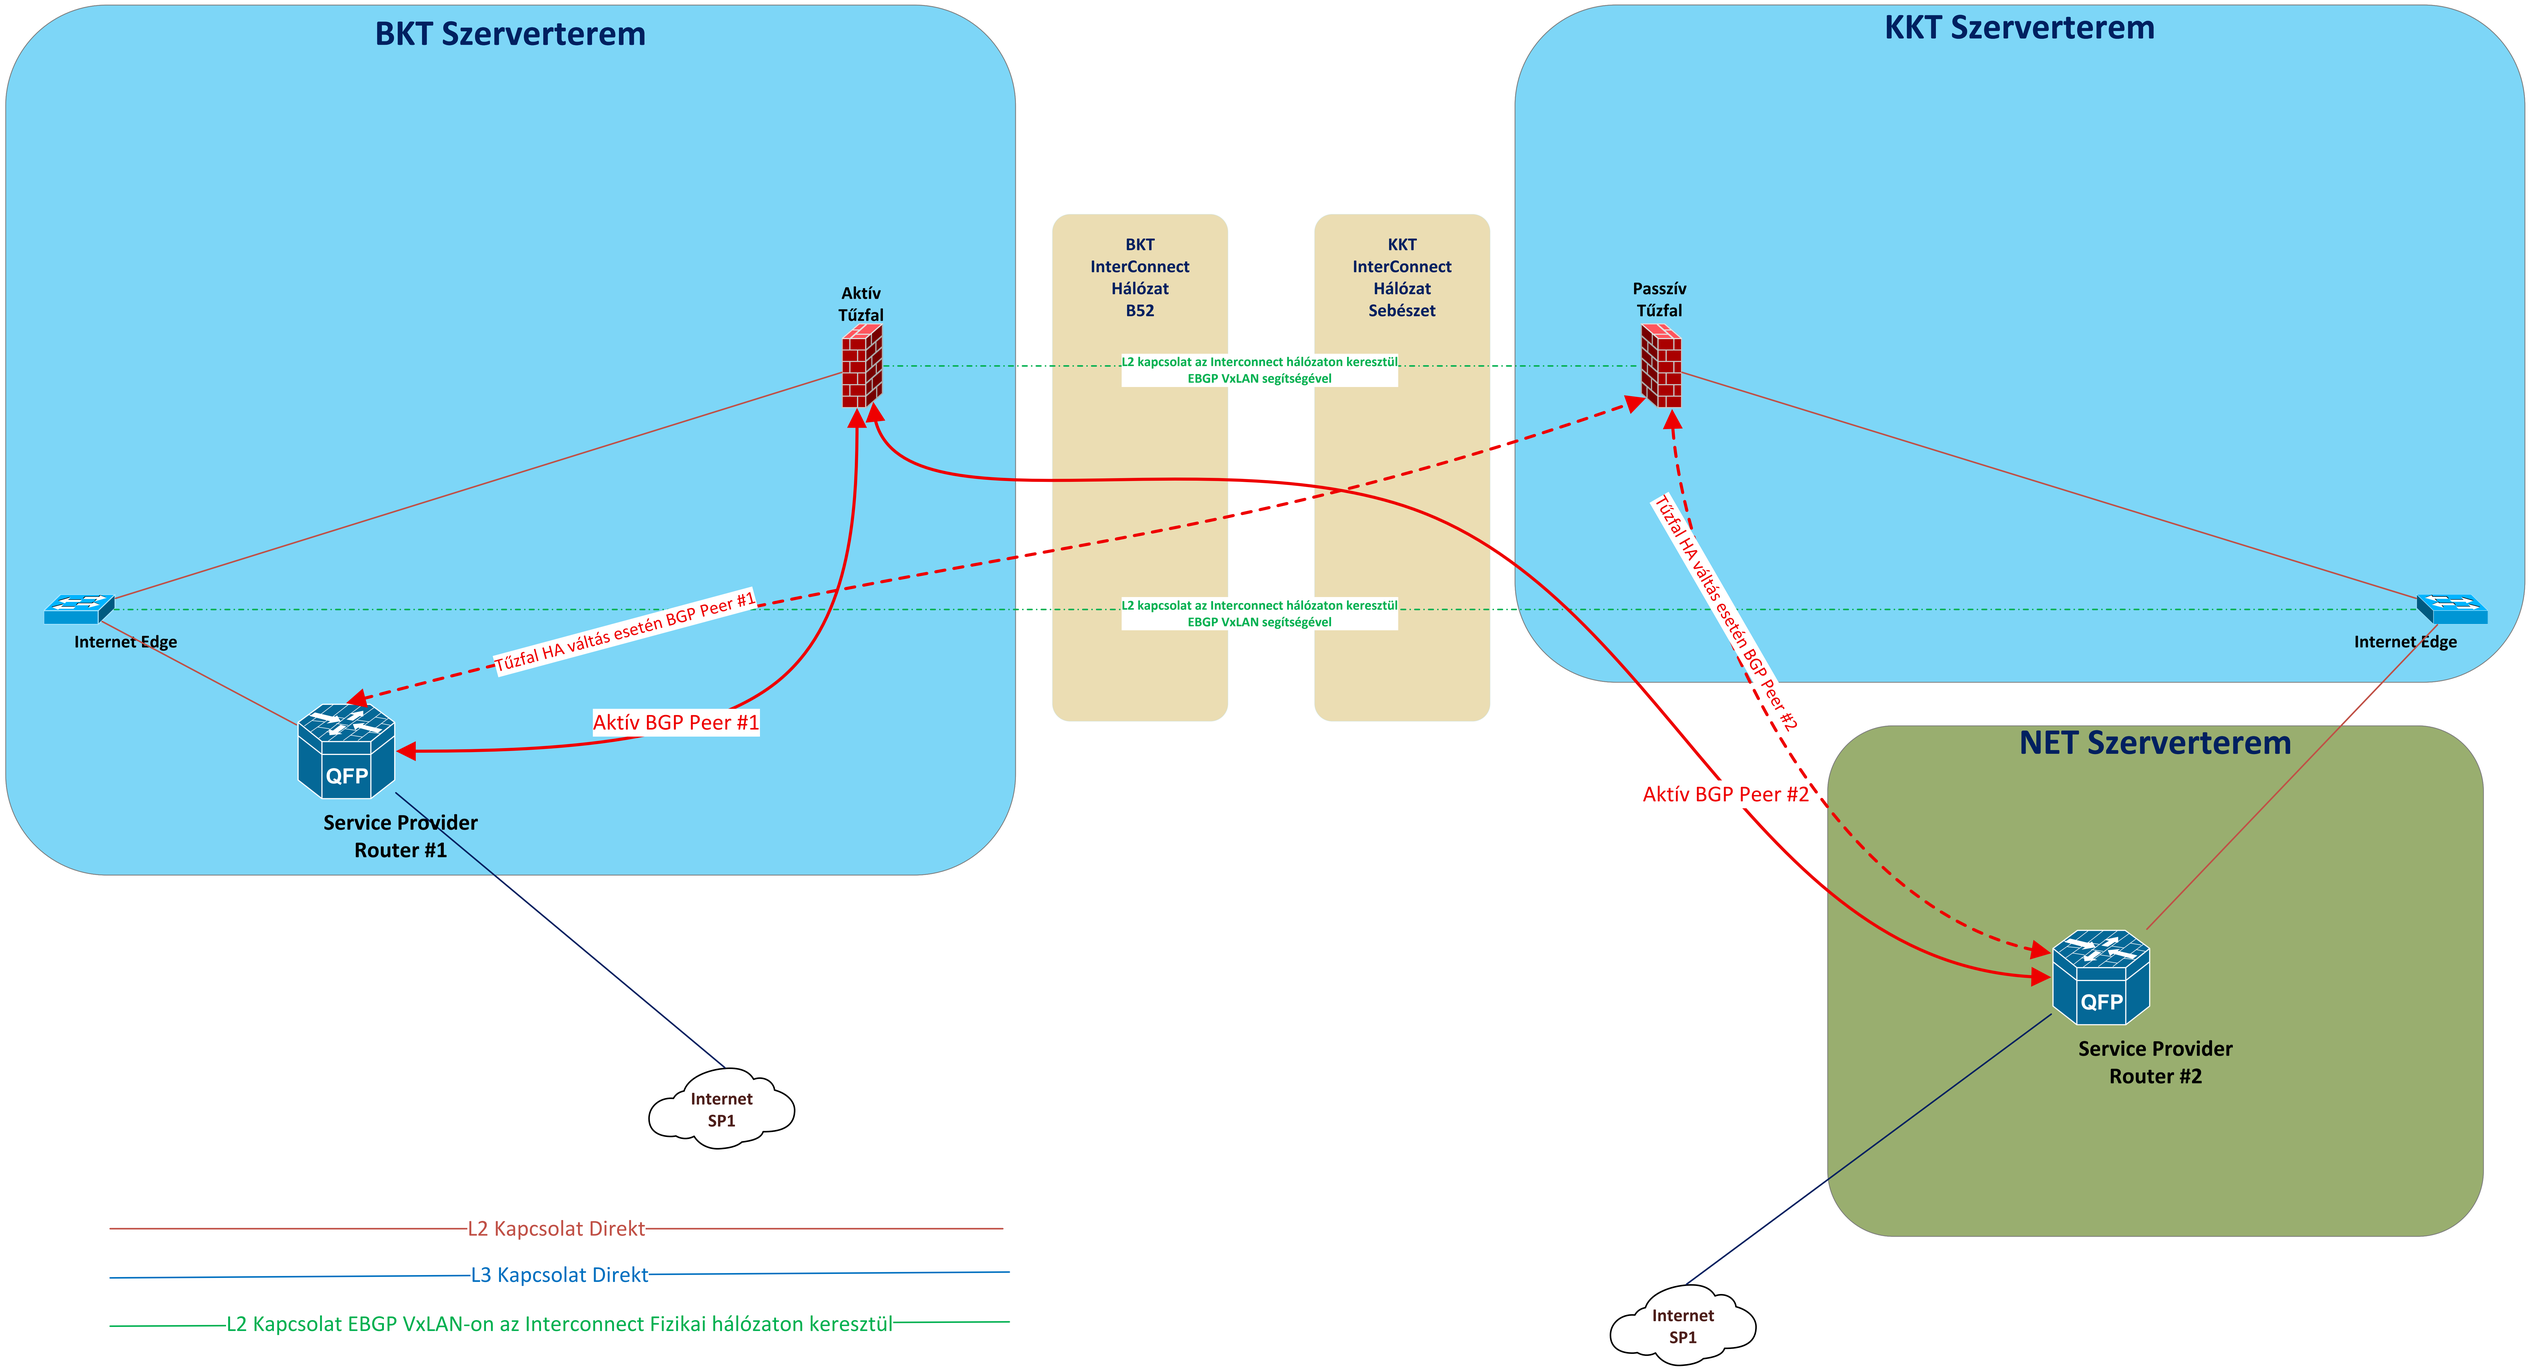
BKT Szerverterem
KKT Szerverterem
BKT InterConnect Hálózat B52
KKT InterConnect Hálózat Sebészet
Aktív Tűzfal
Passzív Tűzfal
L2 kapcsolat az Interconnect hálózaton keresztül EBGP VxLAN segítségével
L2 kapcsolat az Interconnect hálózaton keresztül EBGP VxLAN segítségével
Internet Edge
Internet Edge
Tűzfal HA váltás esetén BGP Peer #1
Tűzfal HA váltás esetén BGP Peer #2
Aktív BGP Peer #1
Aktív BGP Peer #2
QFP
Service Provider Router #1
NET Szerverterem
QFP
Service Provider Router #2
Internet SP1
Internet SP1
L2 Kapcsolat Direkt
L3 Kapcsolat Direkt
L2 Kapcsolat EBGP VxLAN-on az Interconnect Fizikai hálózaton keresztül

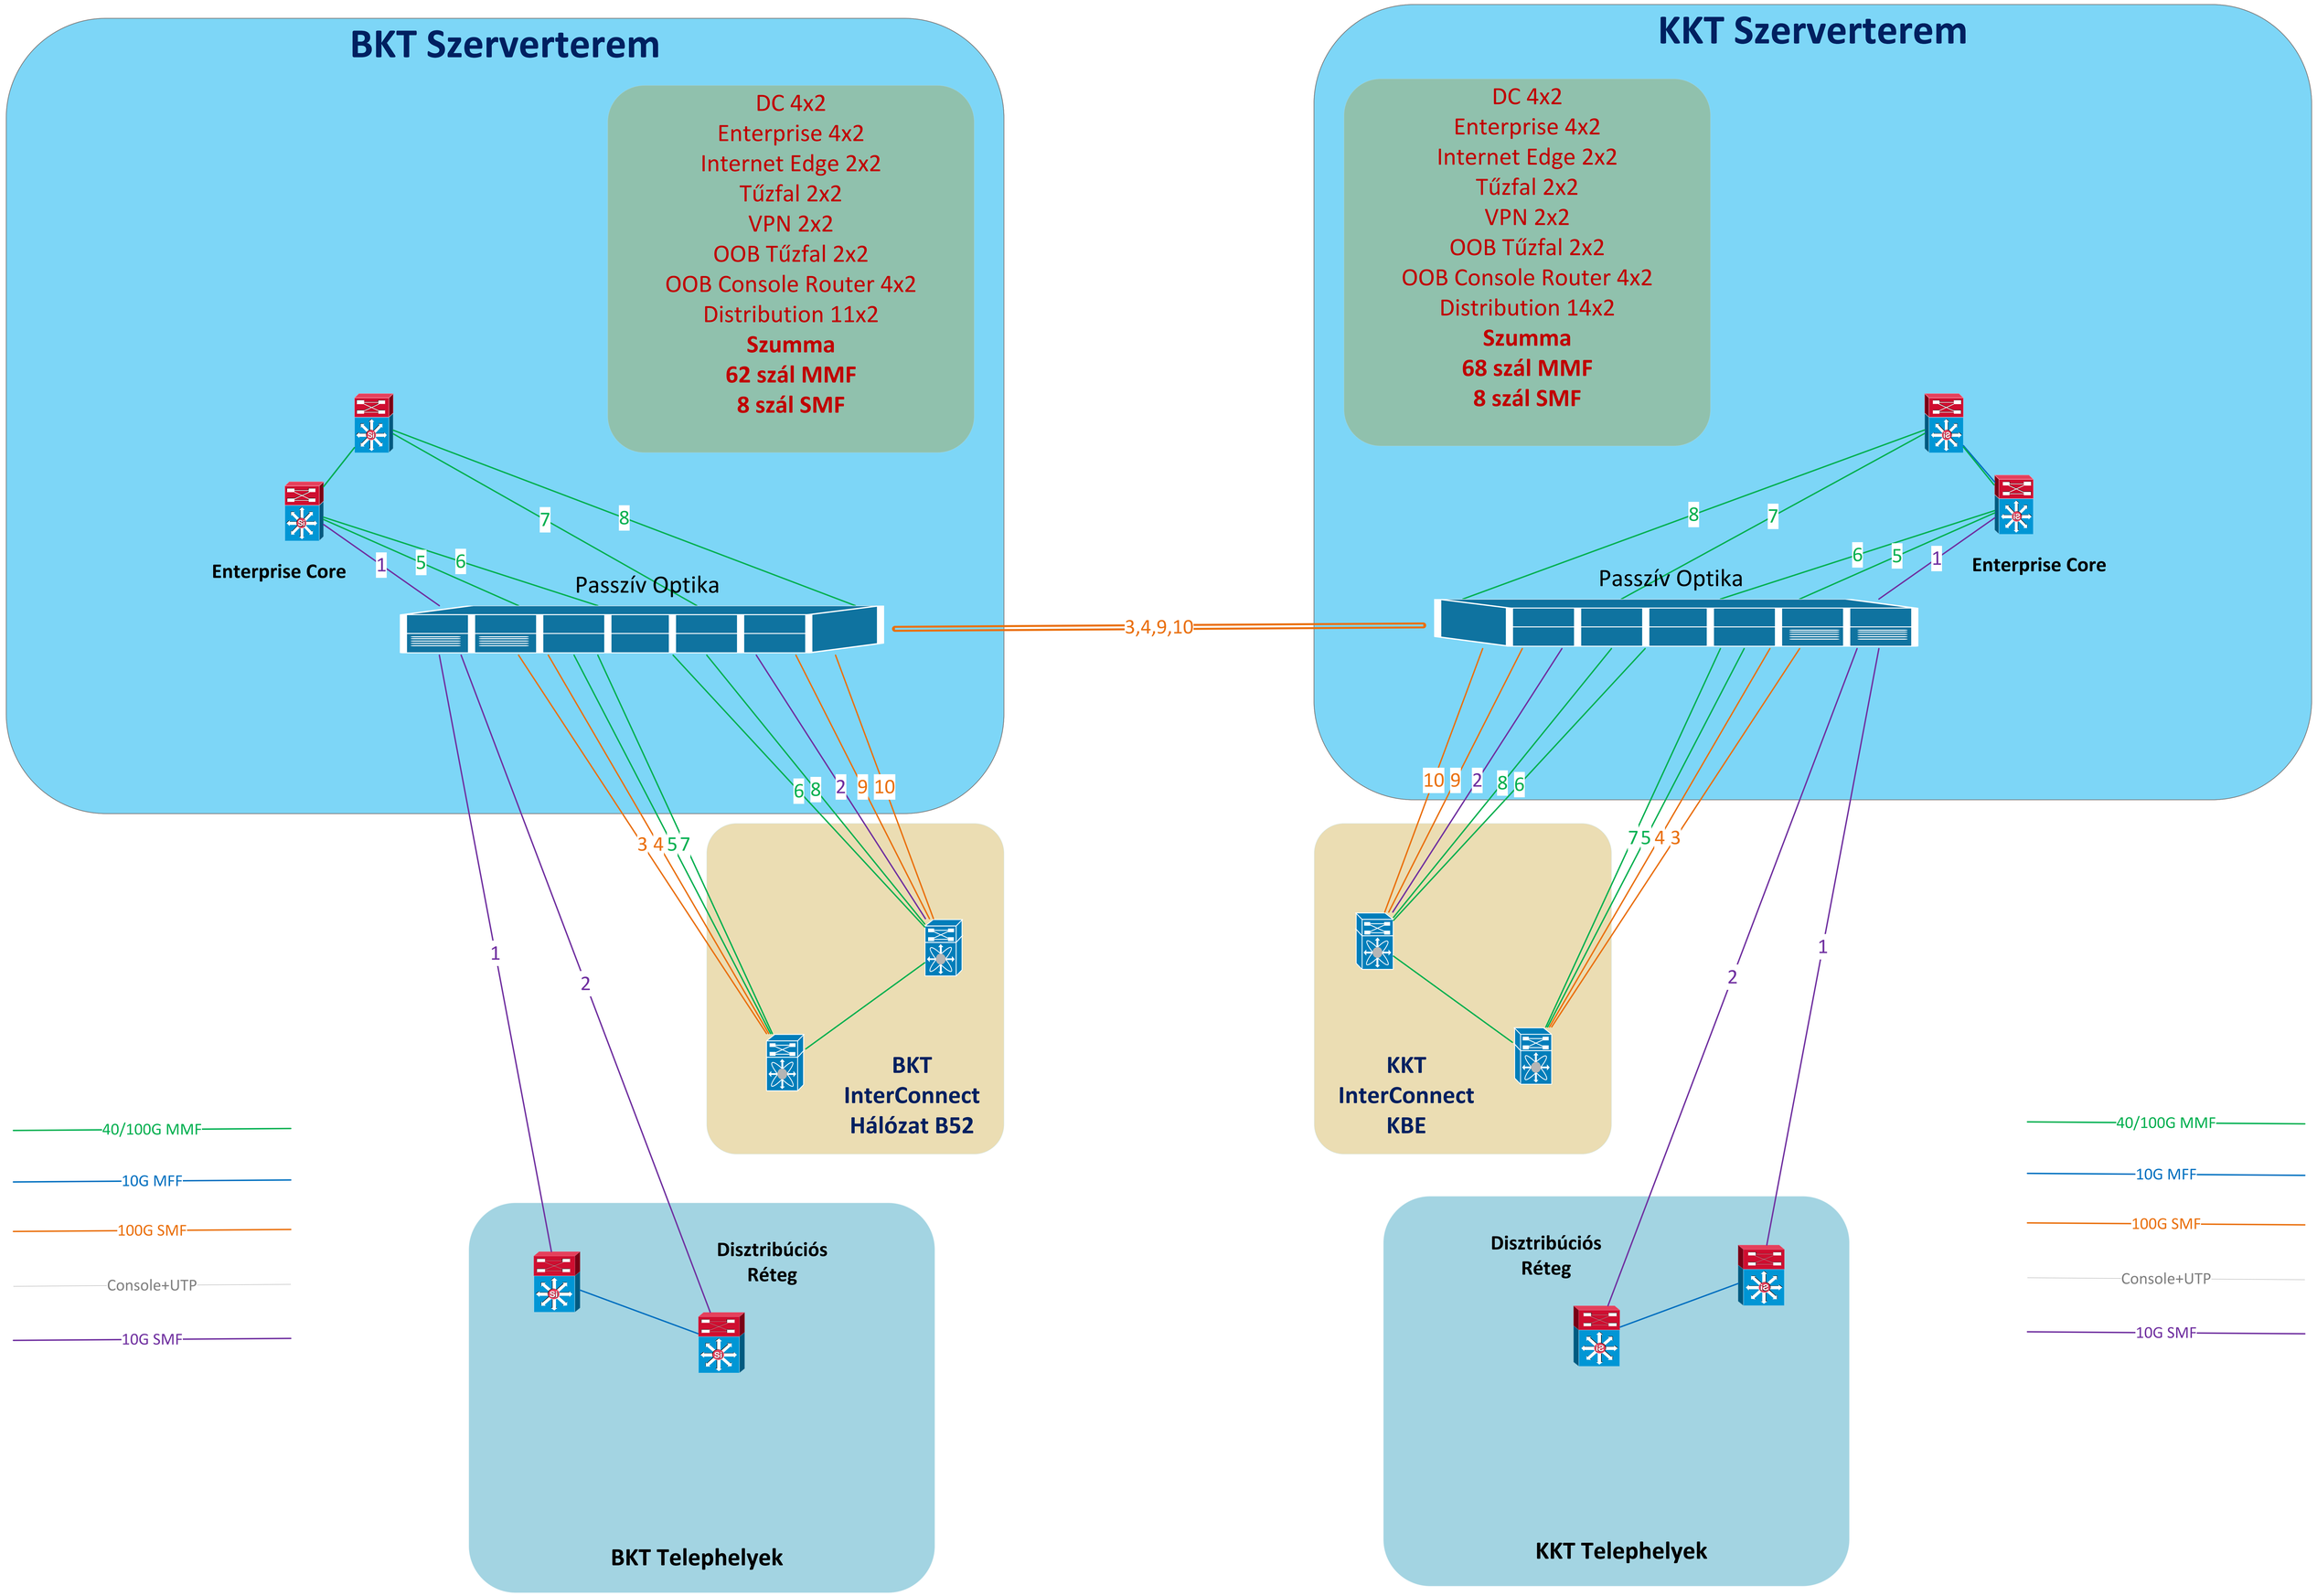
BKT Szerverterem
DC 4x2
Enterprise 4x2
Internet Edge 2x2
Tűzfal 2x2
VPN 2x2
OOB Tűzfal 2x2
OOB Console Router 4x2
Distribution 11x2
Szumma
62 szál MMF
8 szál SMF
Enterprise Core
Passzív Optika
KKT Szerverterem
DC 4x2
Enterprise 4x2
Internet Edge 2x2
Tűzfal 2x2
VPN 2x2
OOB Tűzfal 2x2
OOB Console Router 4x2
Distribution 14x2
Szumma
68 szál MMF
8 szál SMF
Enterprise Core
Passzív Optika
3,4,9,10
BKT InterConnect Hálózat B52
KKT InterConnect KBE
Disztribúciós Réteg
BKT Telephelyek
Disztribúciós Réteg
KKT Telephelyek
40/100G MMF
10G MFF
100G SMF
Console+UTP
10G SMF
40/100G MMF
10G MFF
100G SMF
Console+UTP
10G SMF

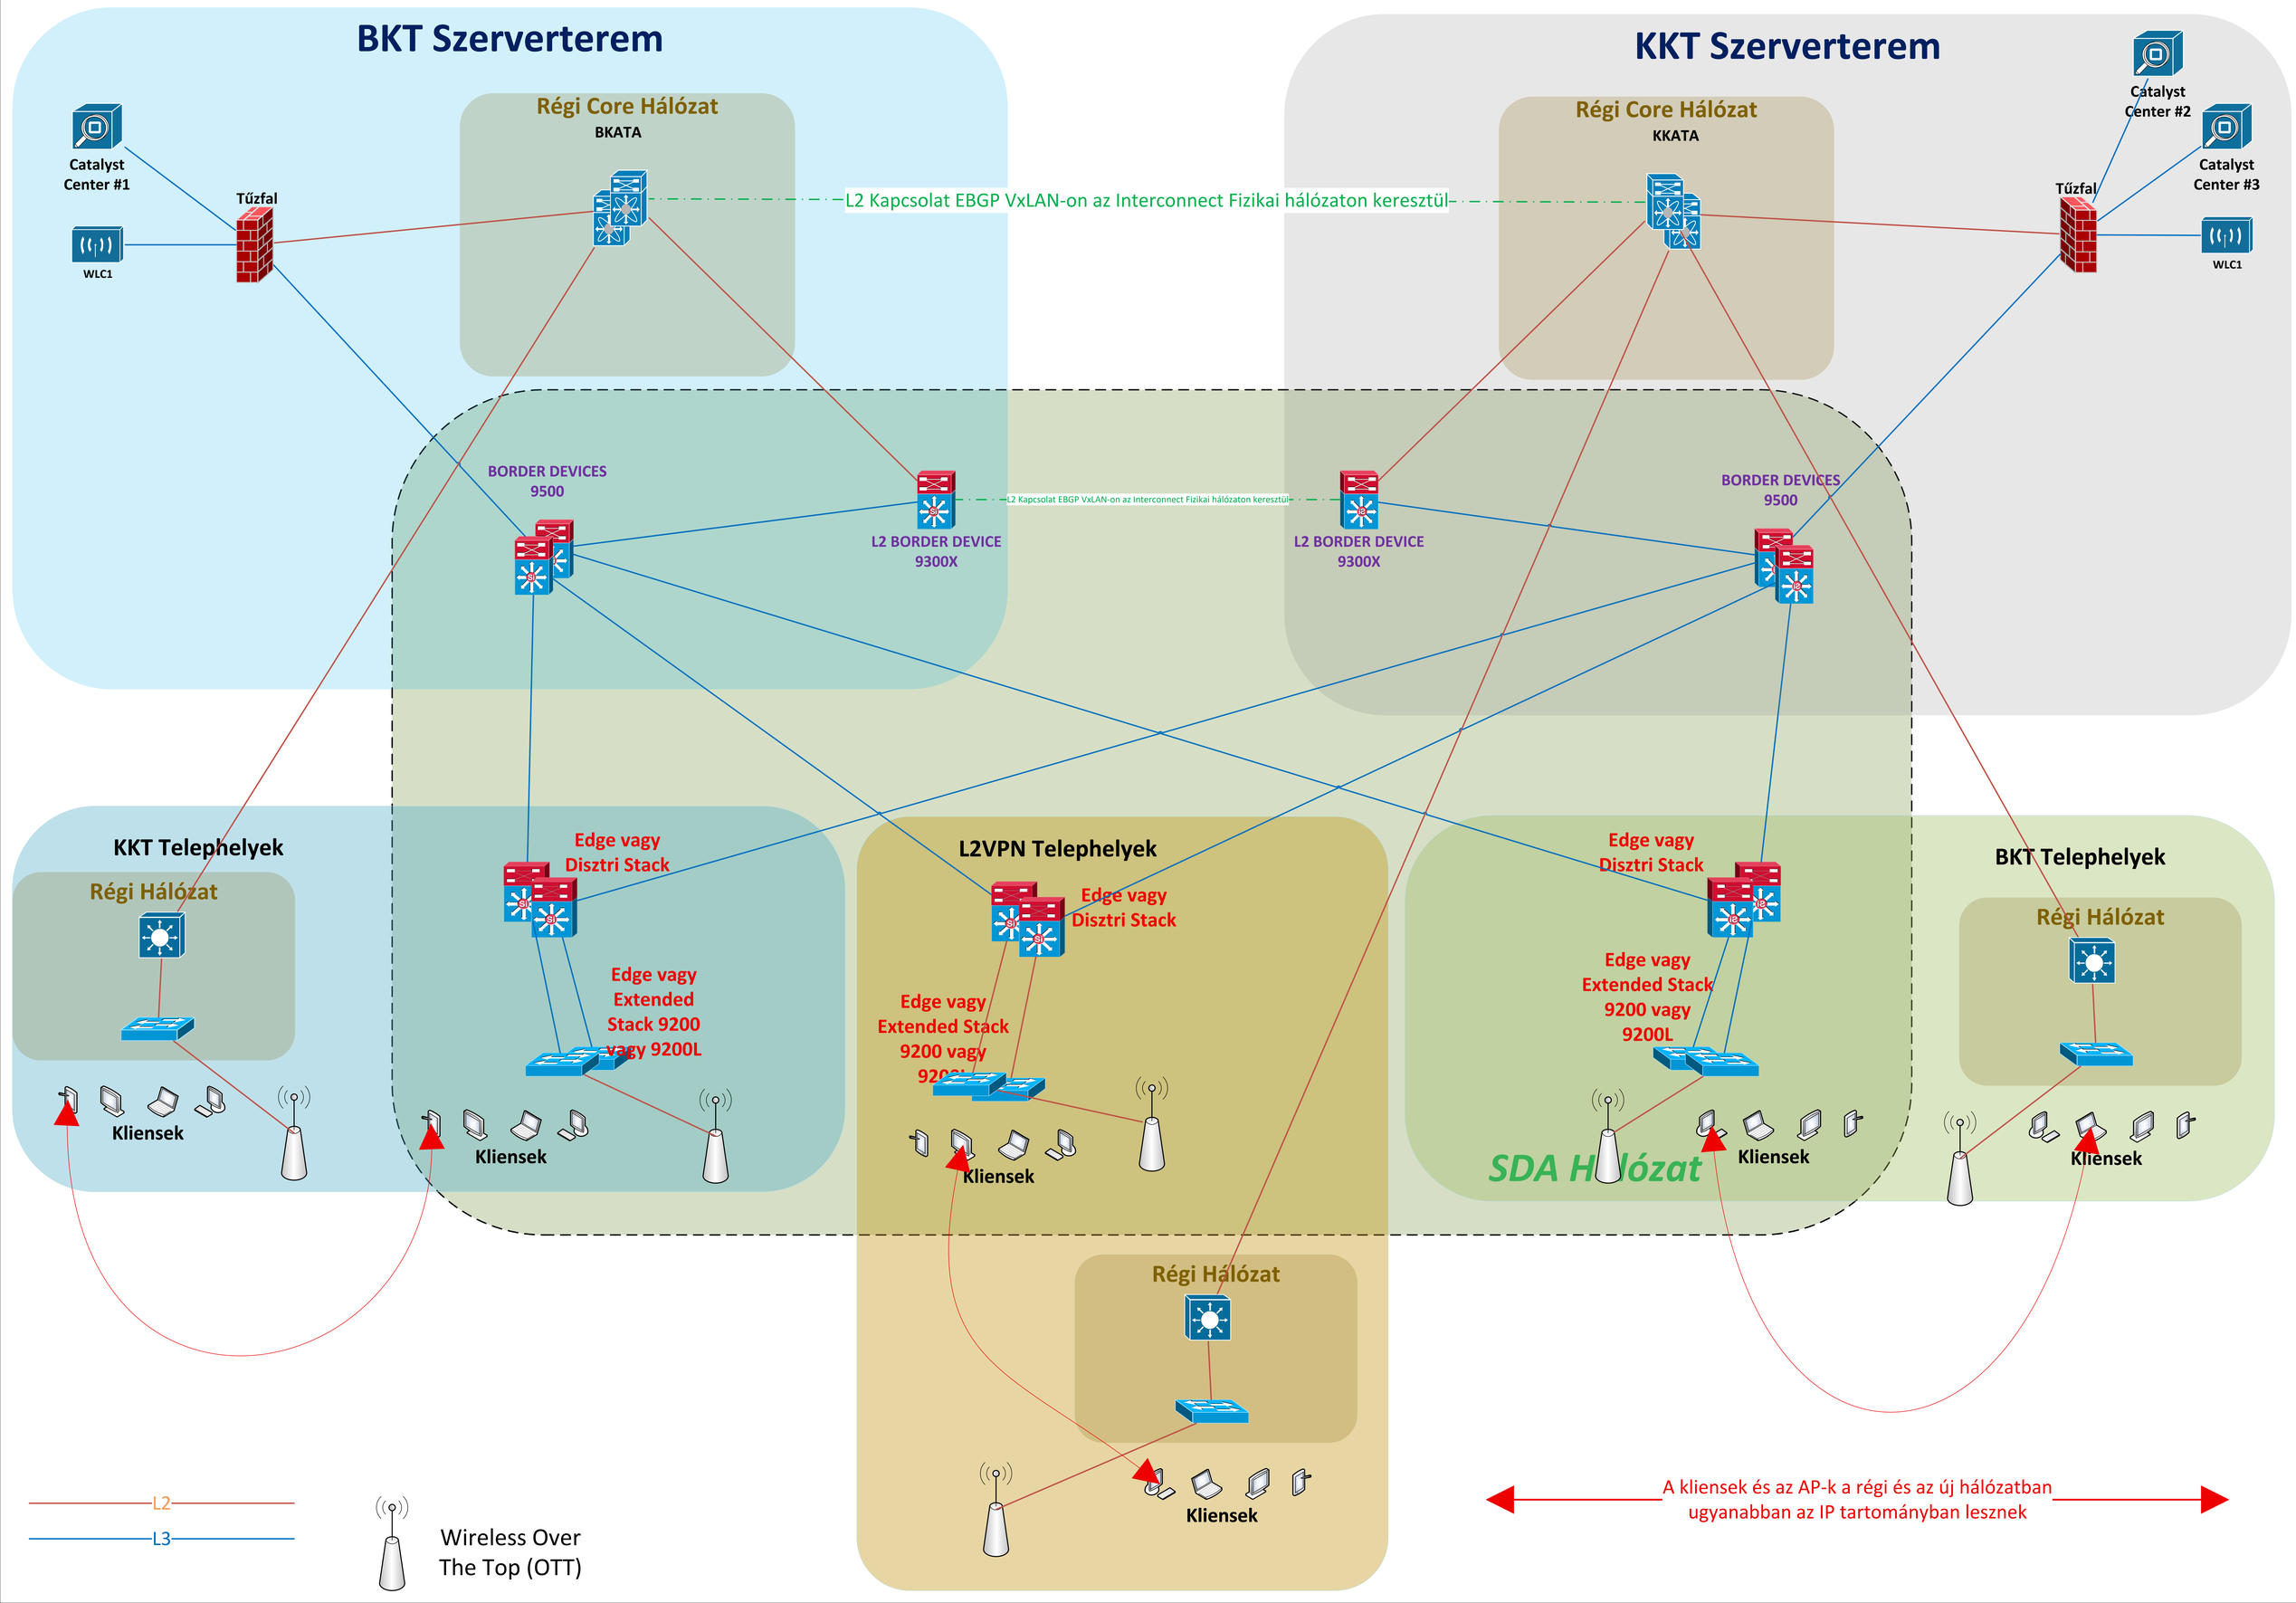
BKT Szerverterem
KKT Szerverterem
Régi Core Hálózat
BKATA
Régi Core Hálózat
KKATA
Catalyst Center #1
WLC1
Tűzfal
L2 Kapcsolat EBGP VxLAN-on az Interconnect Fizikai hálózaton keresztül
Catalyst Center #2
Catalyst Center #3
Tűzfal
WLC1
BORDER DEVICES 9500
L2 BORDER DEVICE 9300X
L2 Kapcsolat EBGP VxLAN-on az Interconnect Fizikai hálózaton keresztül
L2 BORDER DEVICE 9300X
BORDER DEVICES 9500
KKT Telephelyek
Régi Hálózat
Kliensek
Edge vagy Disztri Stack
Edge vagy Extended Stack 9200 vagy 9200L
Kliensek
L2VPN Telephelyek
Edge vagy Disztri Stack
Edge vagy Extended Stack 9200 vagy 9200L
Kliensek
Régi Hálózat
Kliensek
Edge vagy Disztri Stack
Edge vagy Extended Stack 9200 vagy 9200L
SDA Hálózat
Kliensek
BKT Telephelyek
Régi Hálózat
Kliensek
A kliensek és az AP-k a régi és az új hálózatban ugyanabban az IP tartományban lesznek
L2
L3
Wireless Over The Top (OTT)